






Unit type 'E'
without balcony

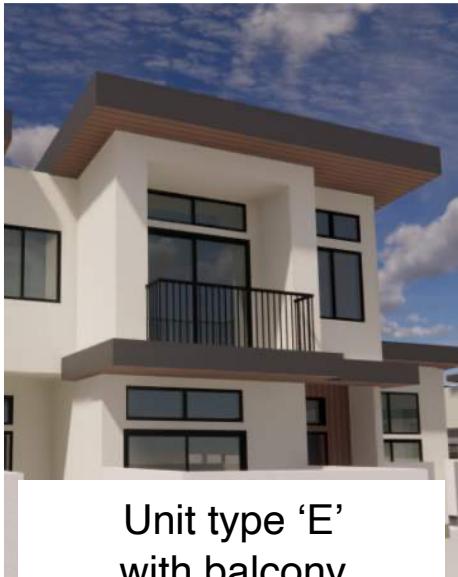


Unit type 'E'
with balcony

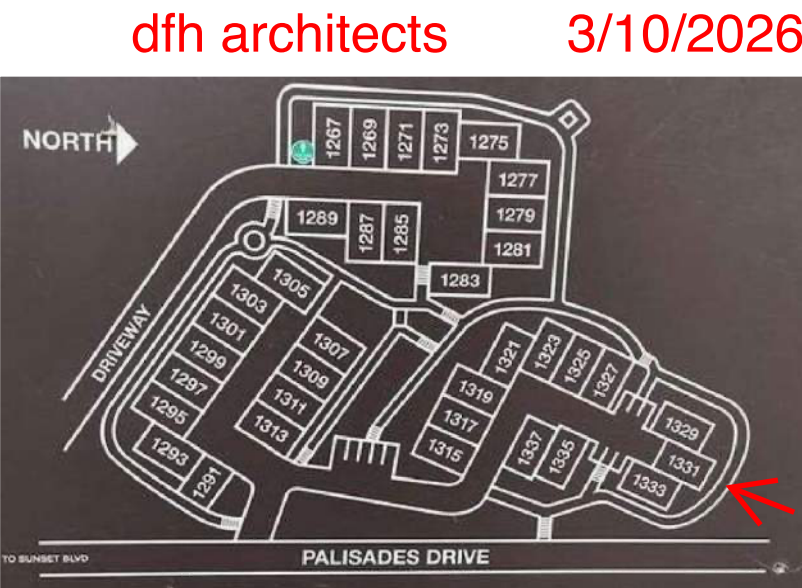


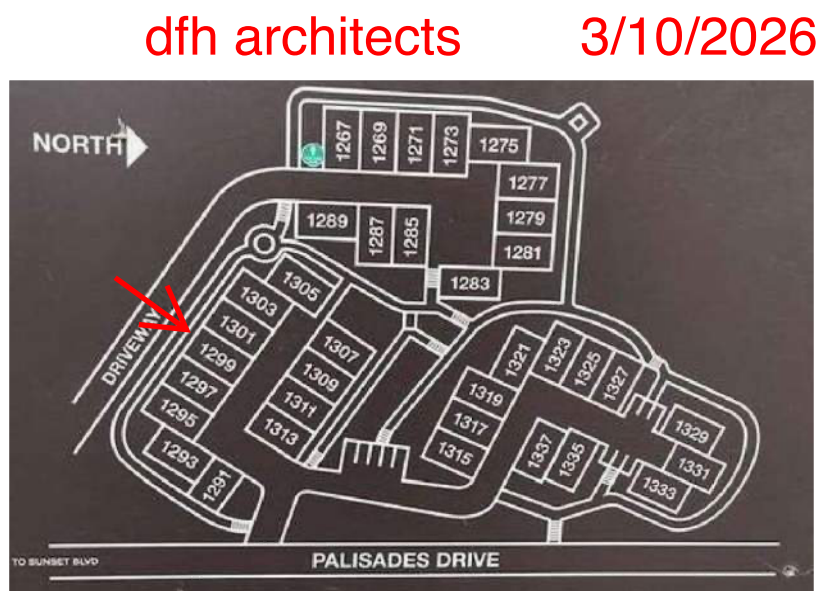


3/10/2026 1:40:08 PM

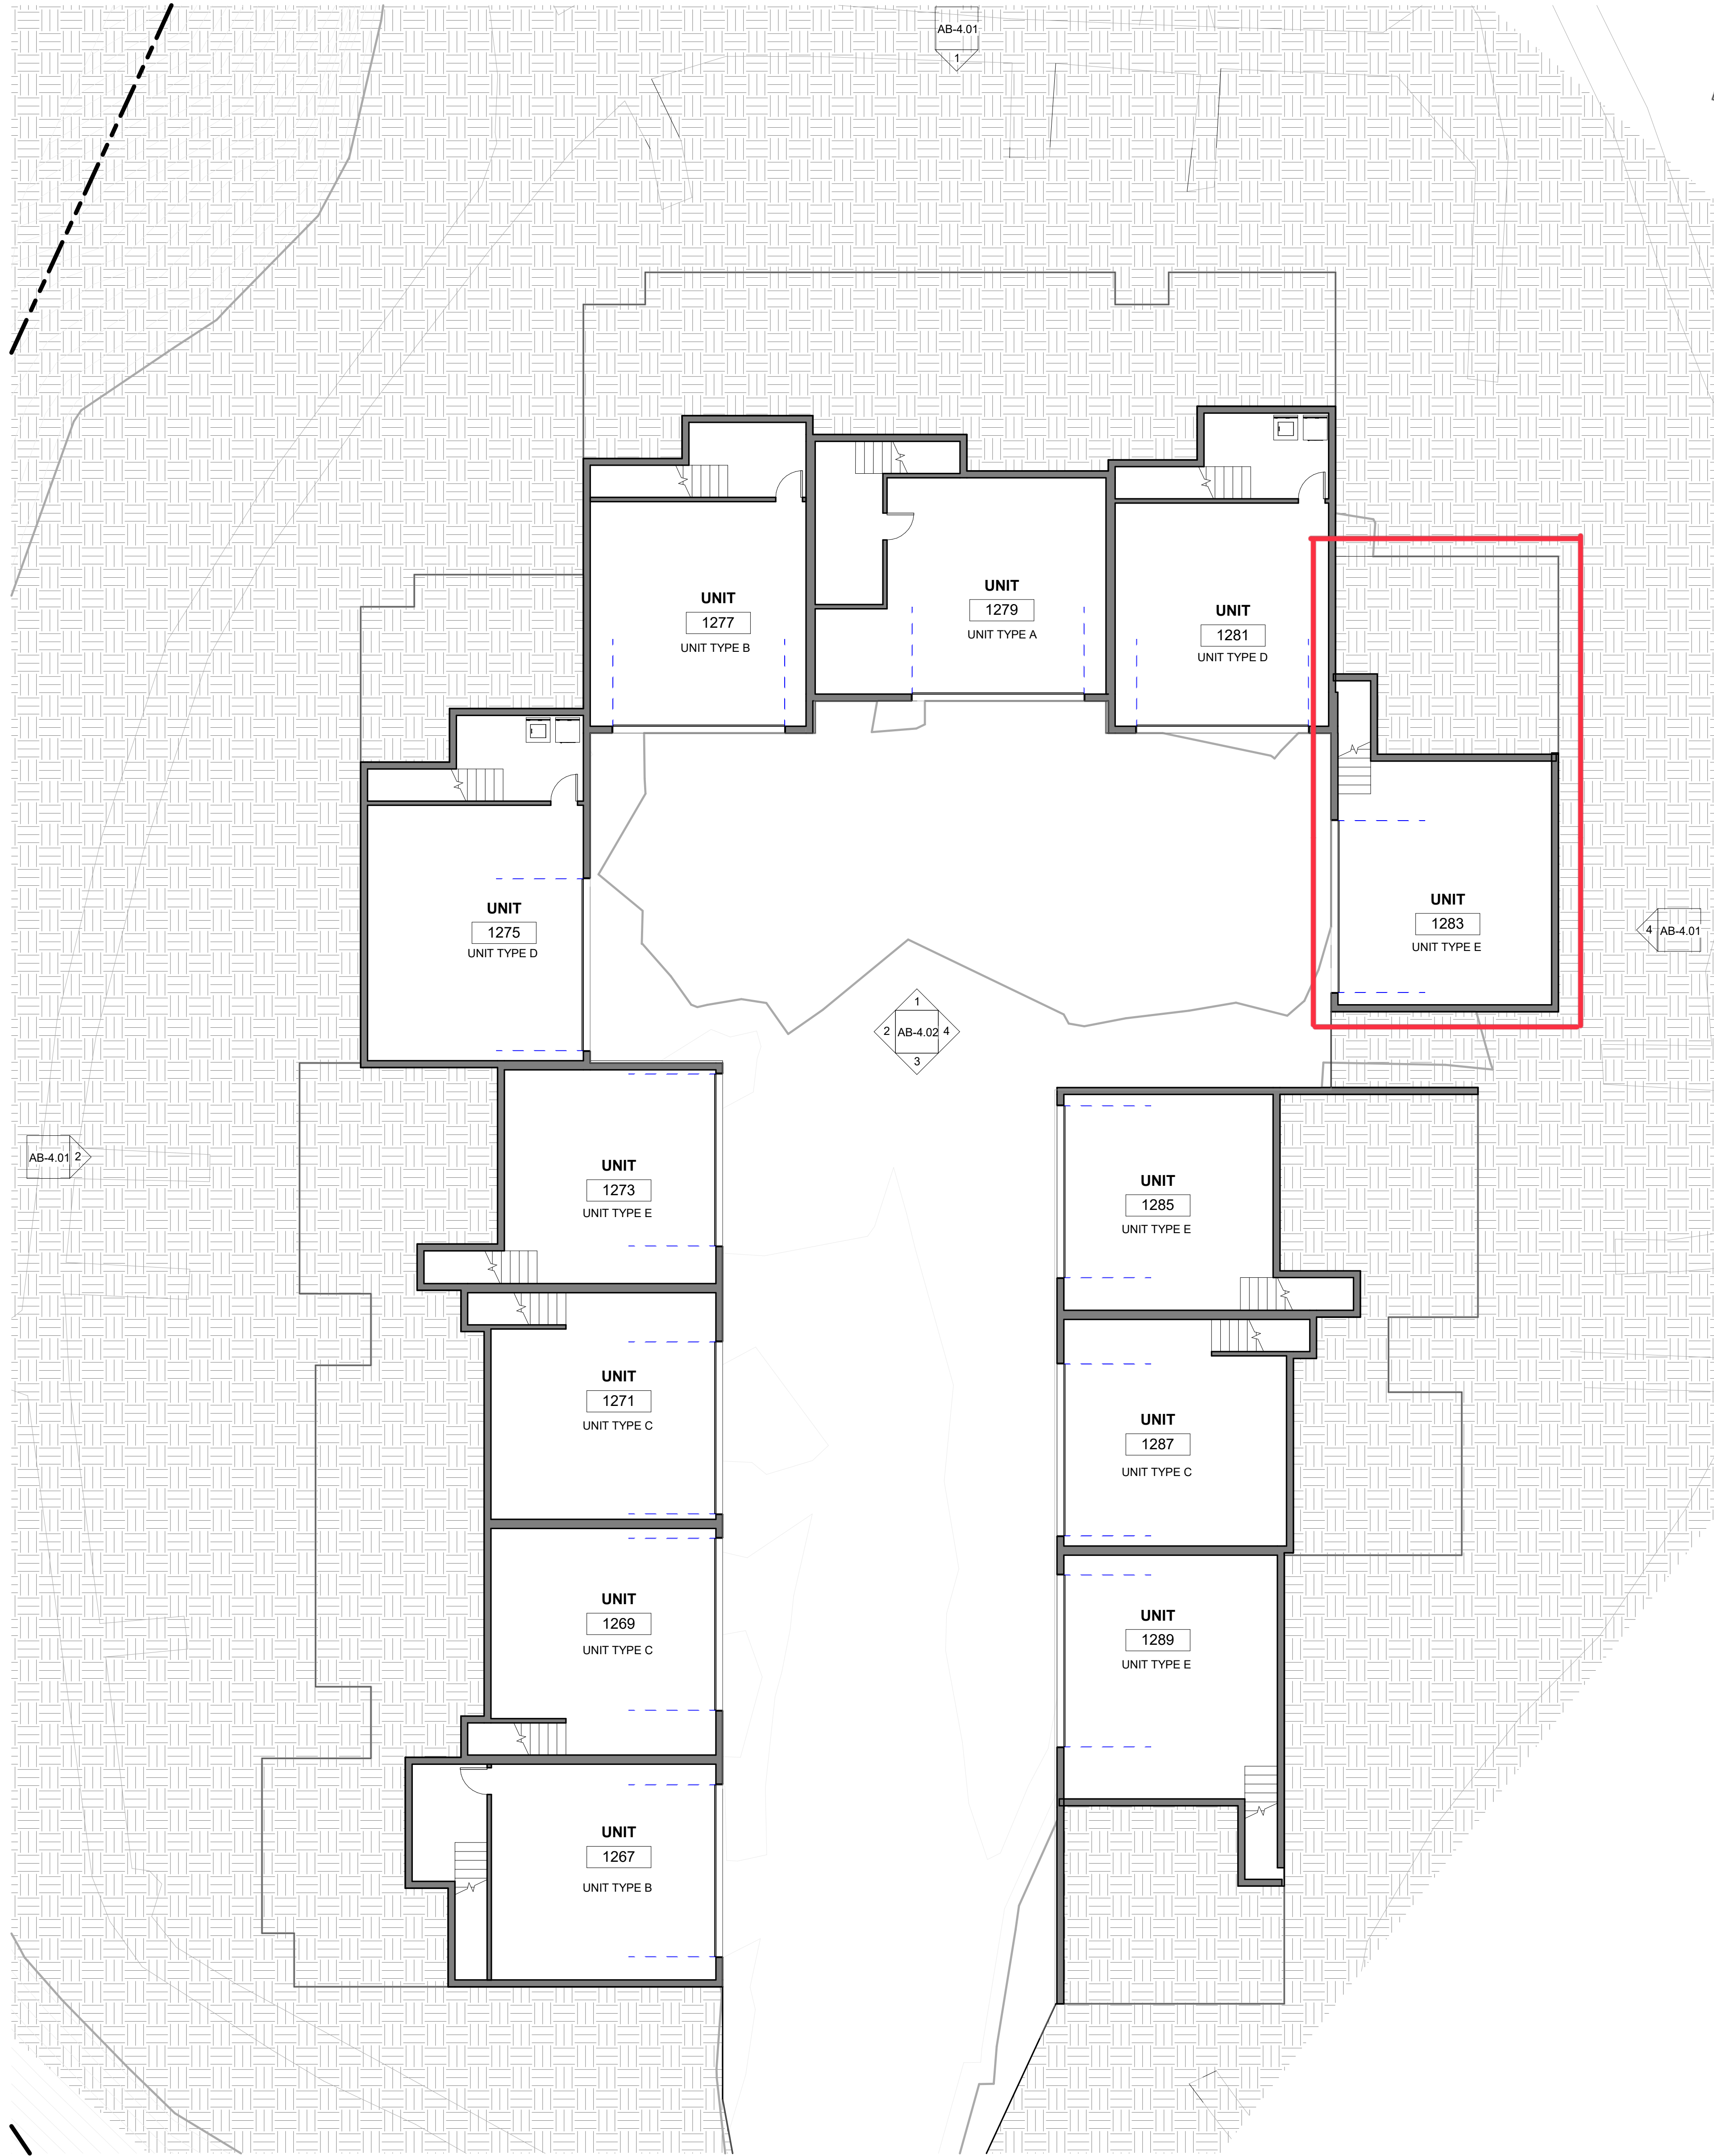

GARAGE LEVEL @ BLDG 8

SCALE:
1/8" = 1'-0"

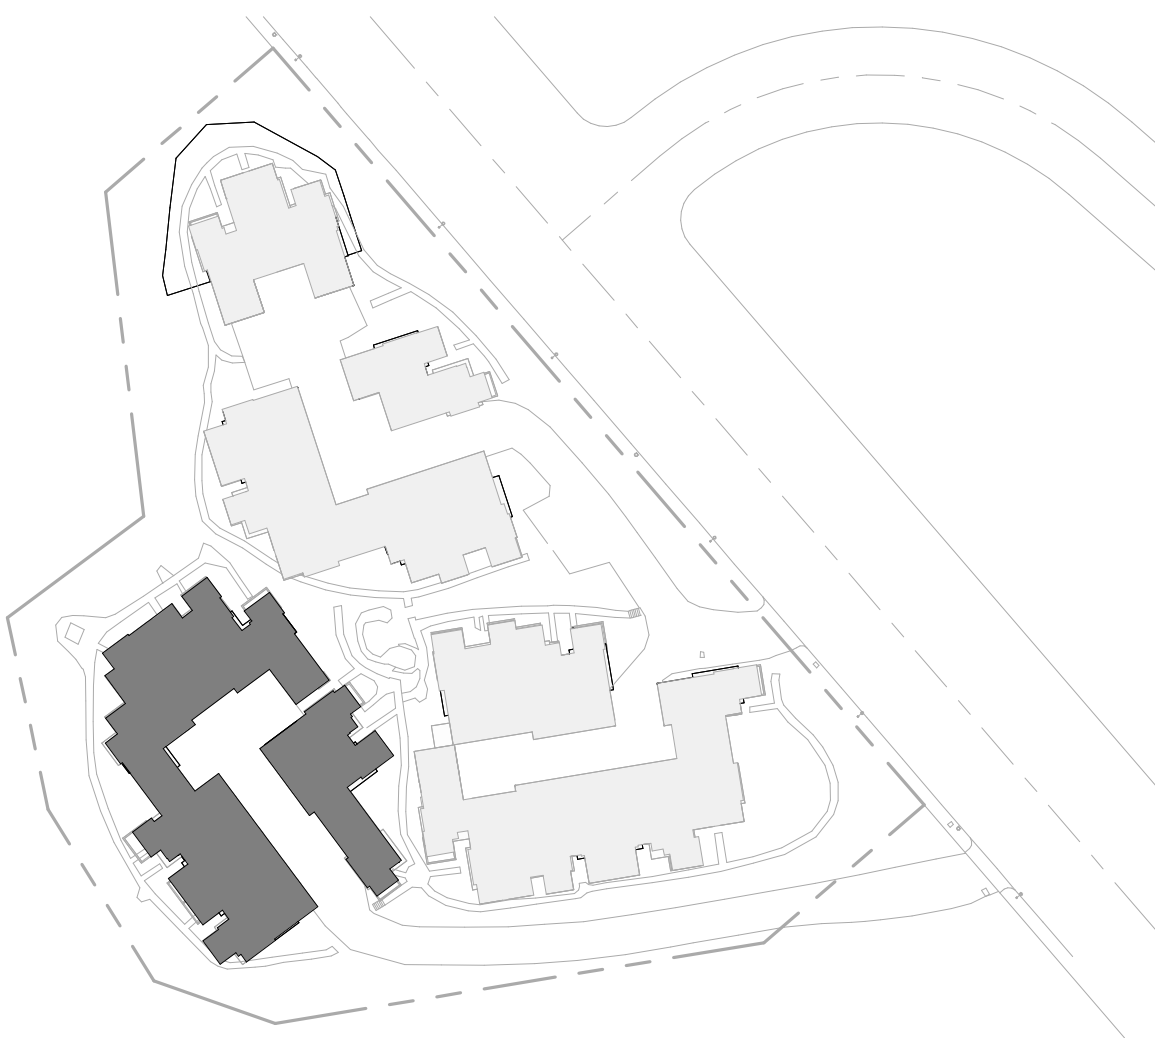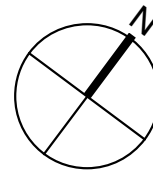


KEY PLAN

3/10/2026 SD OPTION 2 PROGRESS SET



SYCHOA TOWNHOMES 1267-1337 PALISADES DRIVE PACIFIC PALISADES, CA 90272		100% SCHEMATIC DESIGN 2/19/2026		GARAGE LEVEL @ BLDG 8		AB-2.01	
dfh architecture interior environments		1344 20th Street S4, CA 1-931-394-4043 info@dfhaa.com www.dfhaa.com		Scale: As indicated		By: Author	
				Project No: 2532			

3/10/2026 1:40:10 PM

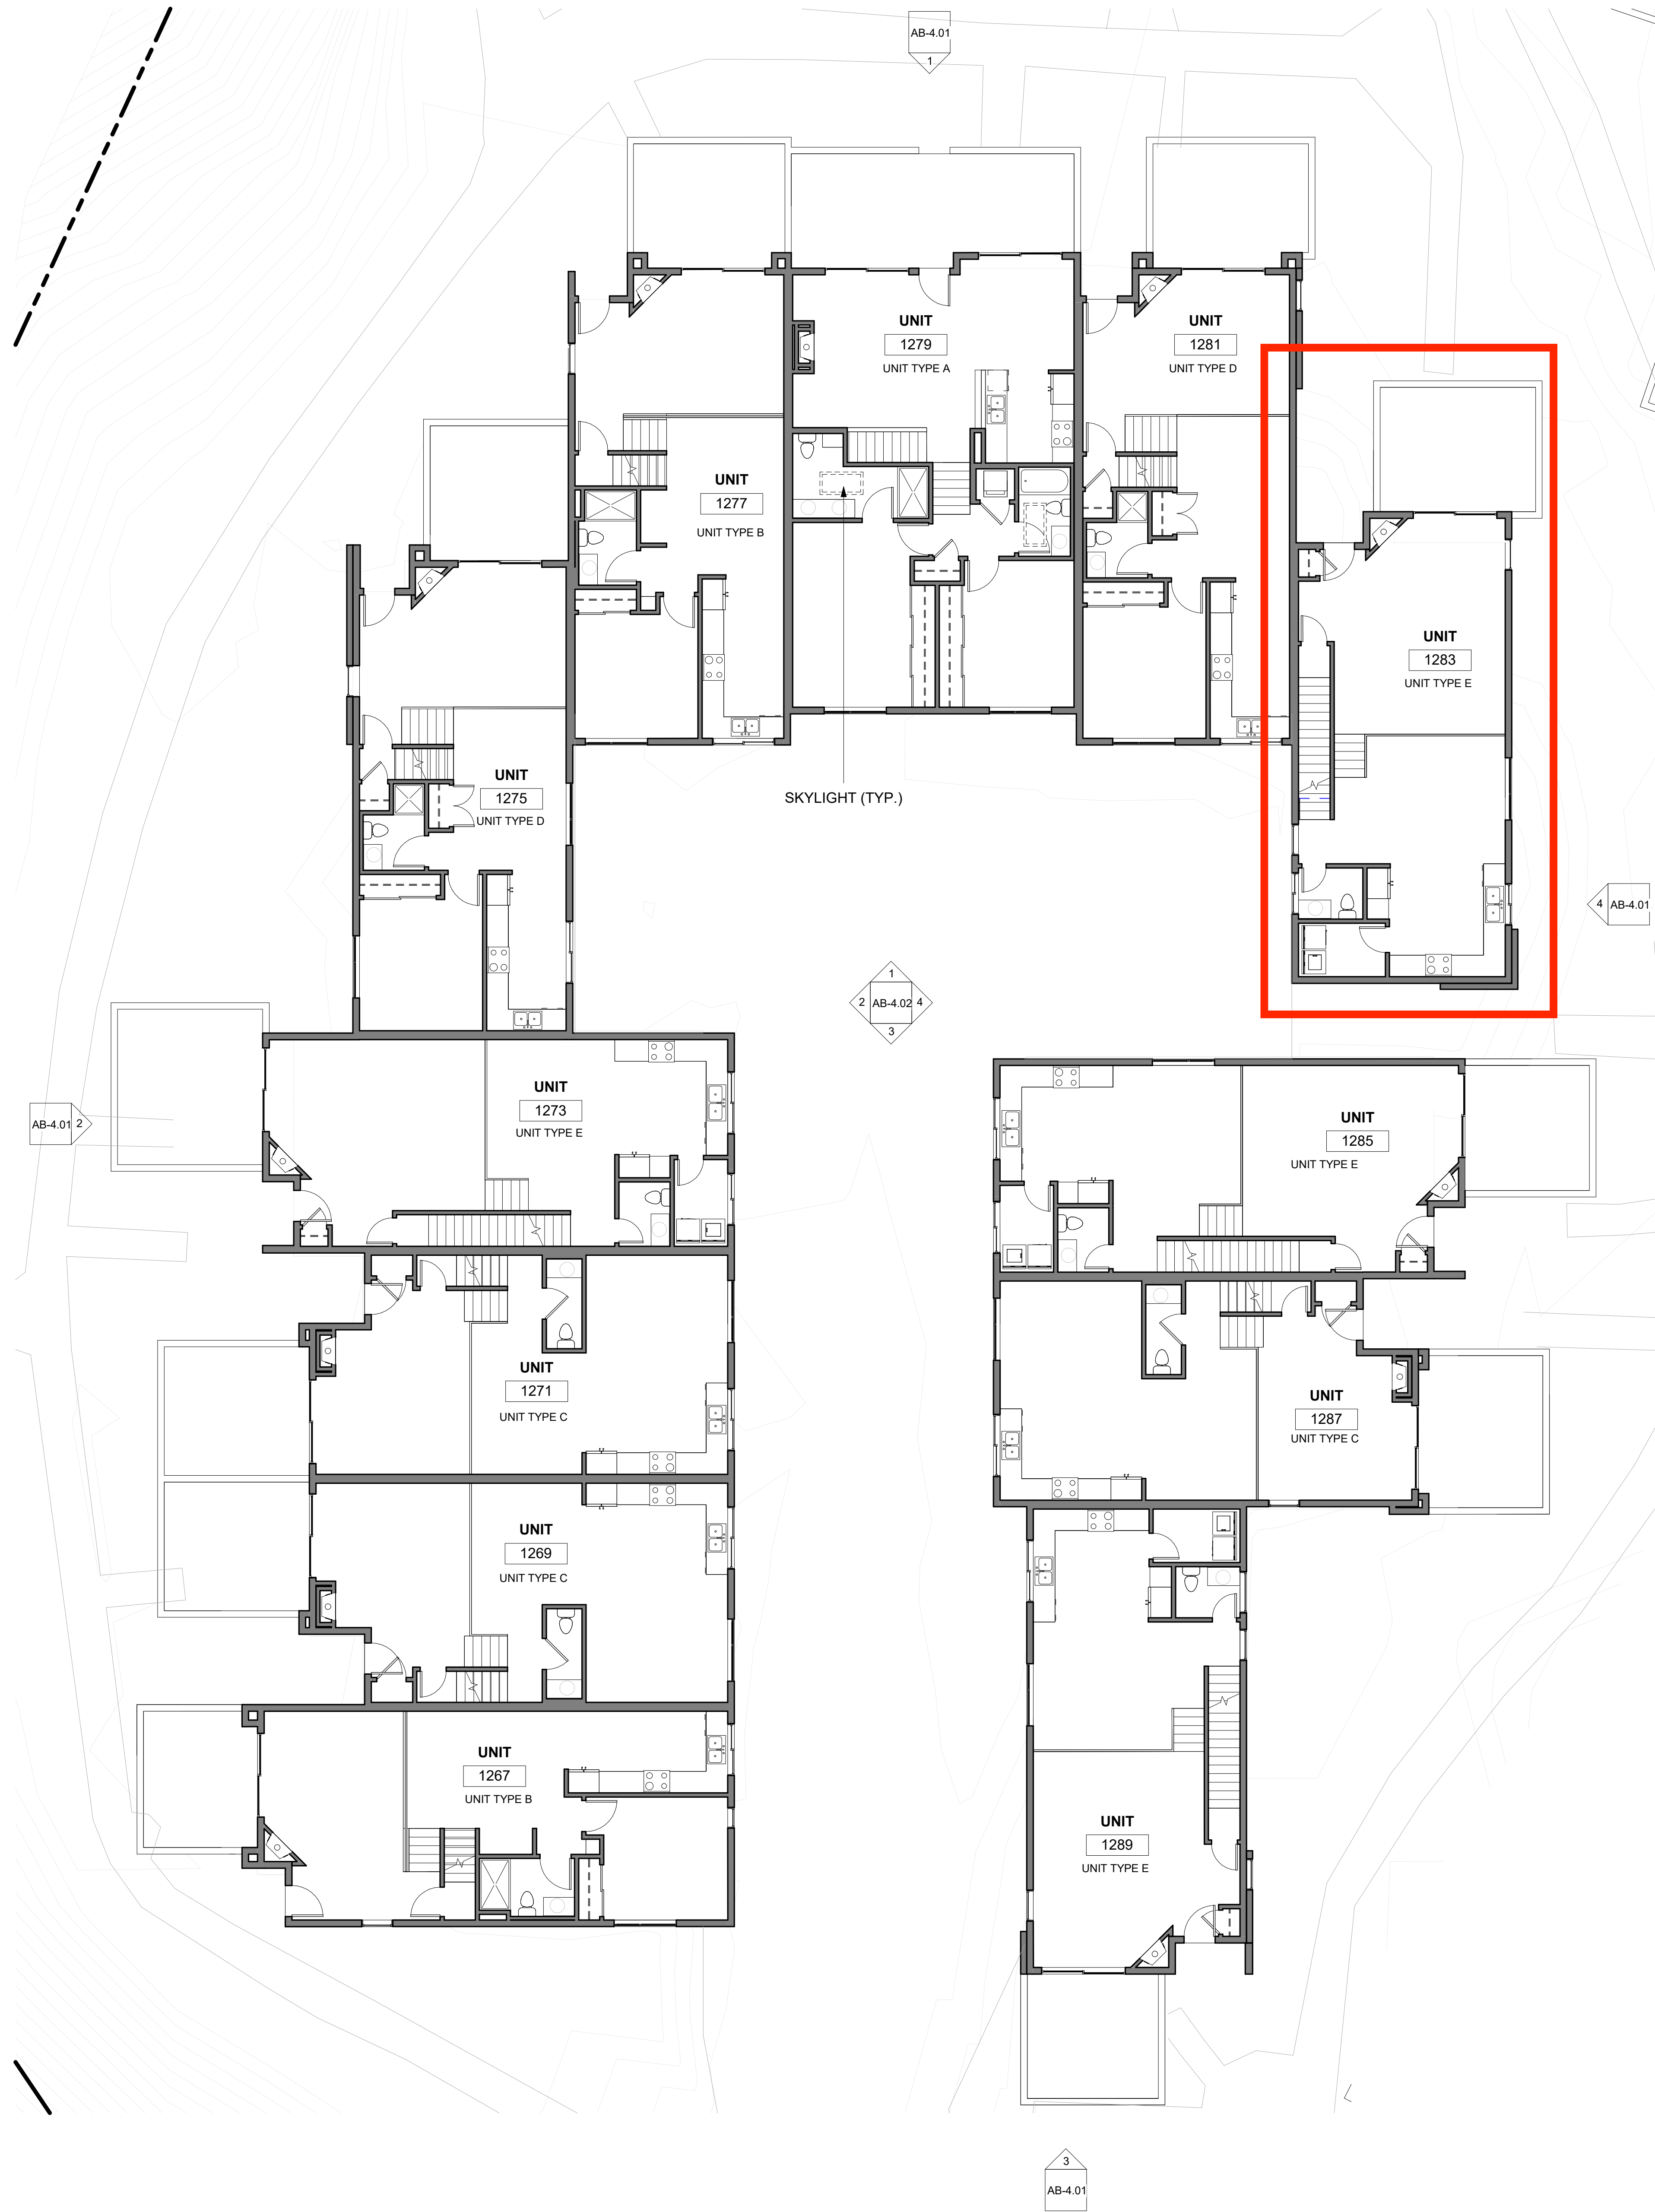

1ST FLOOR/GROUND LEVEL @ BLDG 8

SCALE:
1/8" = 1'-0"

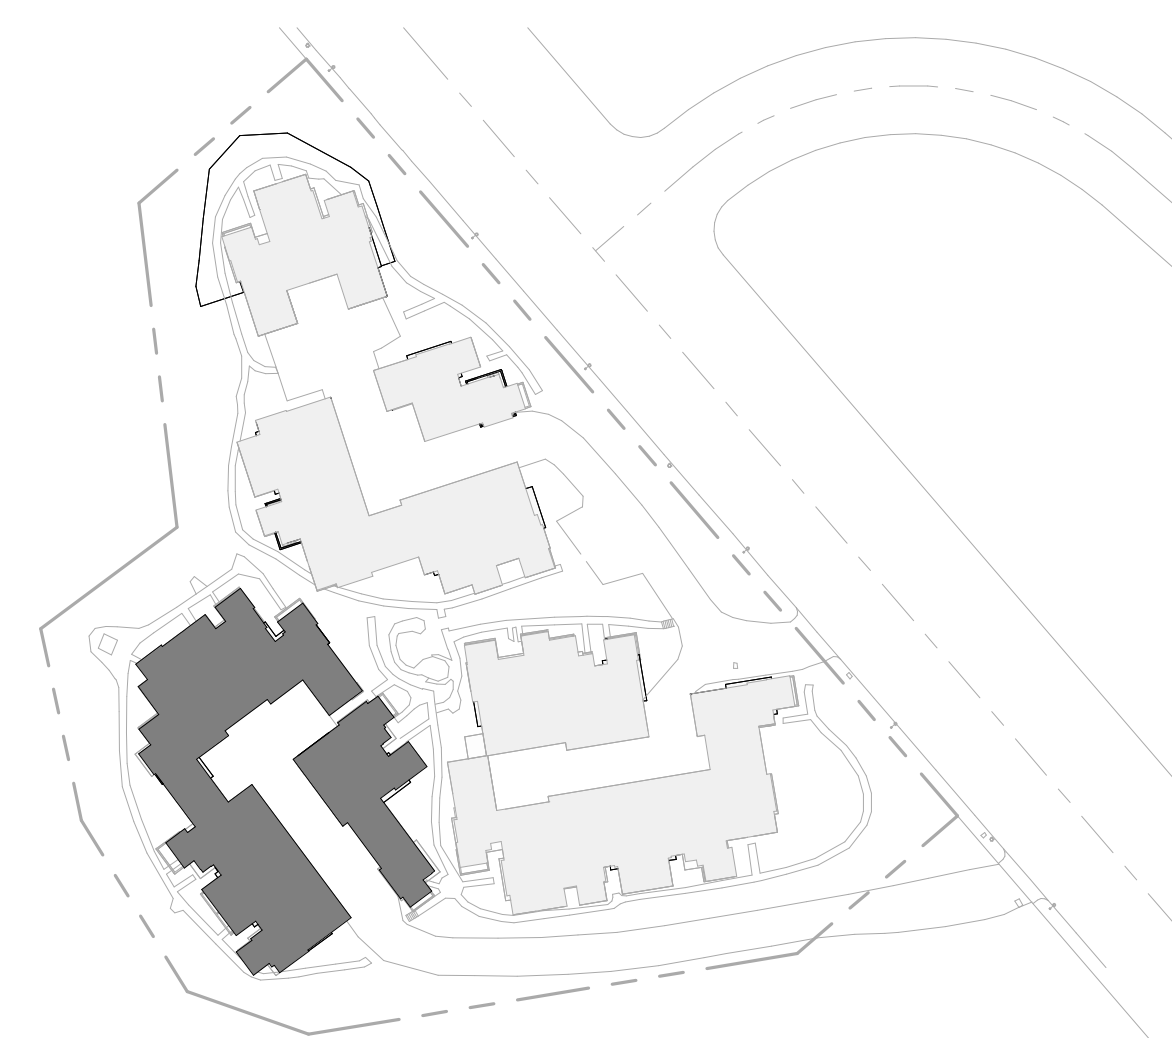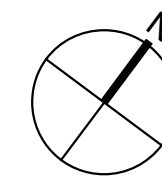

KEY PLAN

3/10/2026 SD OPTION 2 PROGRESS SET

SYCHOA TOWNHOMES
1267-1337 PALISADES DRIVE
PACIFIC PALISADES, CA 90272


100% SCHEMATIC DESIGN
2/19/2026

1ST FLOOR/GROUND
LEVEL @ BLDG 8


Scale:
As indicated
By: Author
Project No:
2532

AB-2.02

3/10/2026 1:40:11 PM

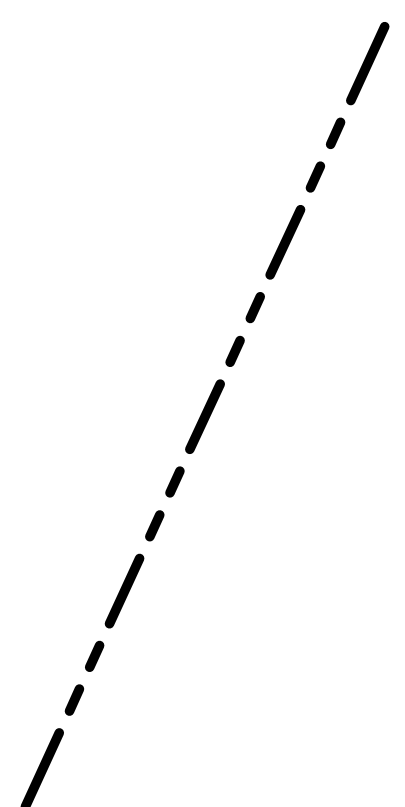


AB-4.01 2

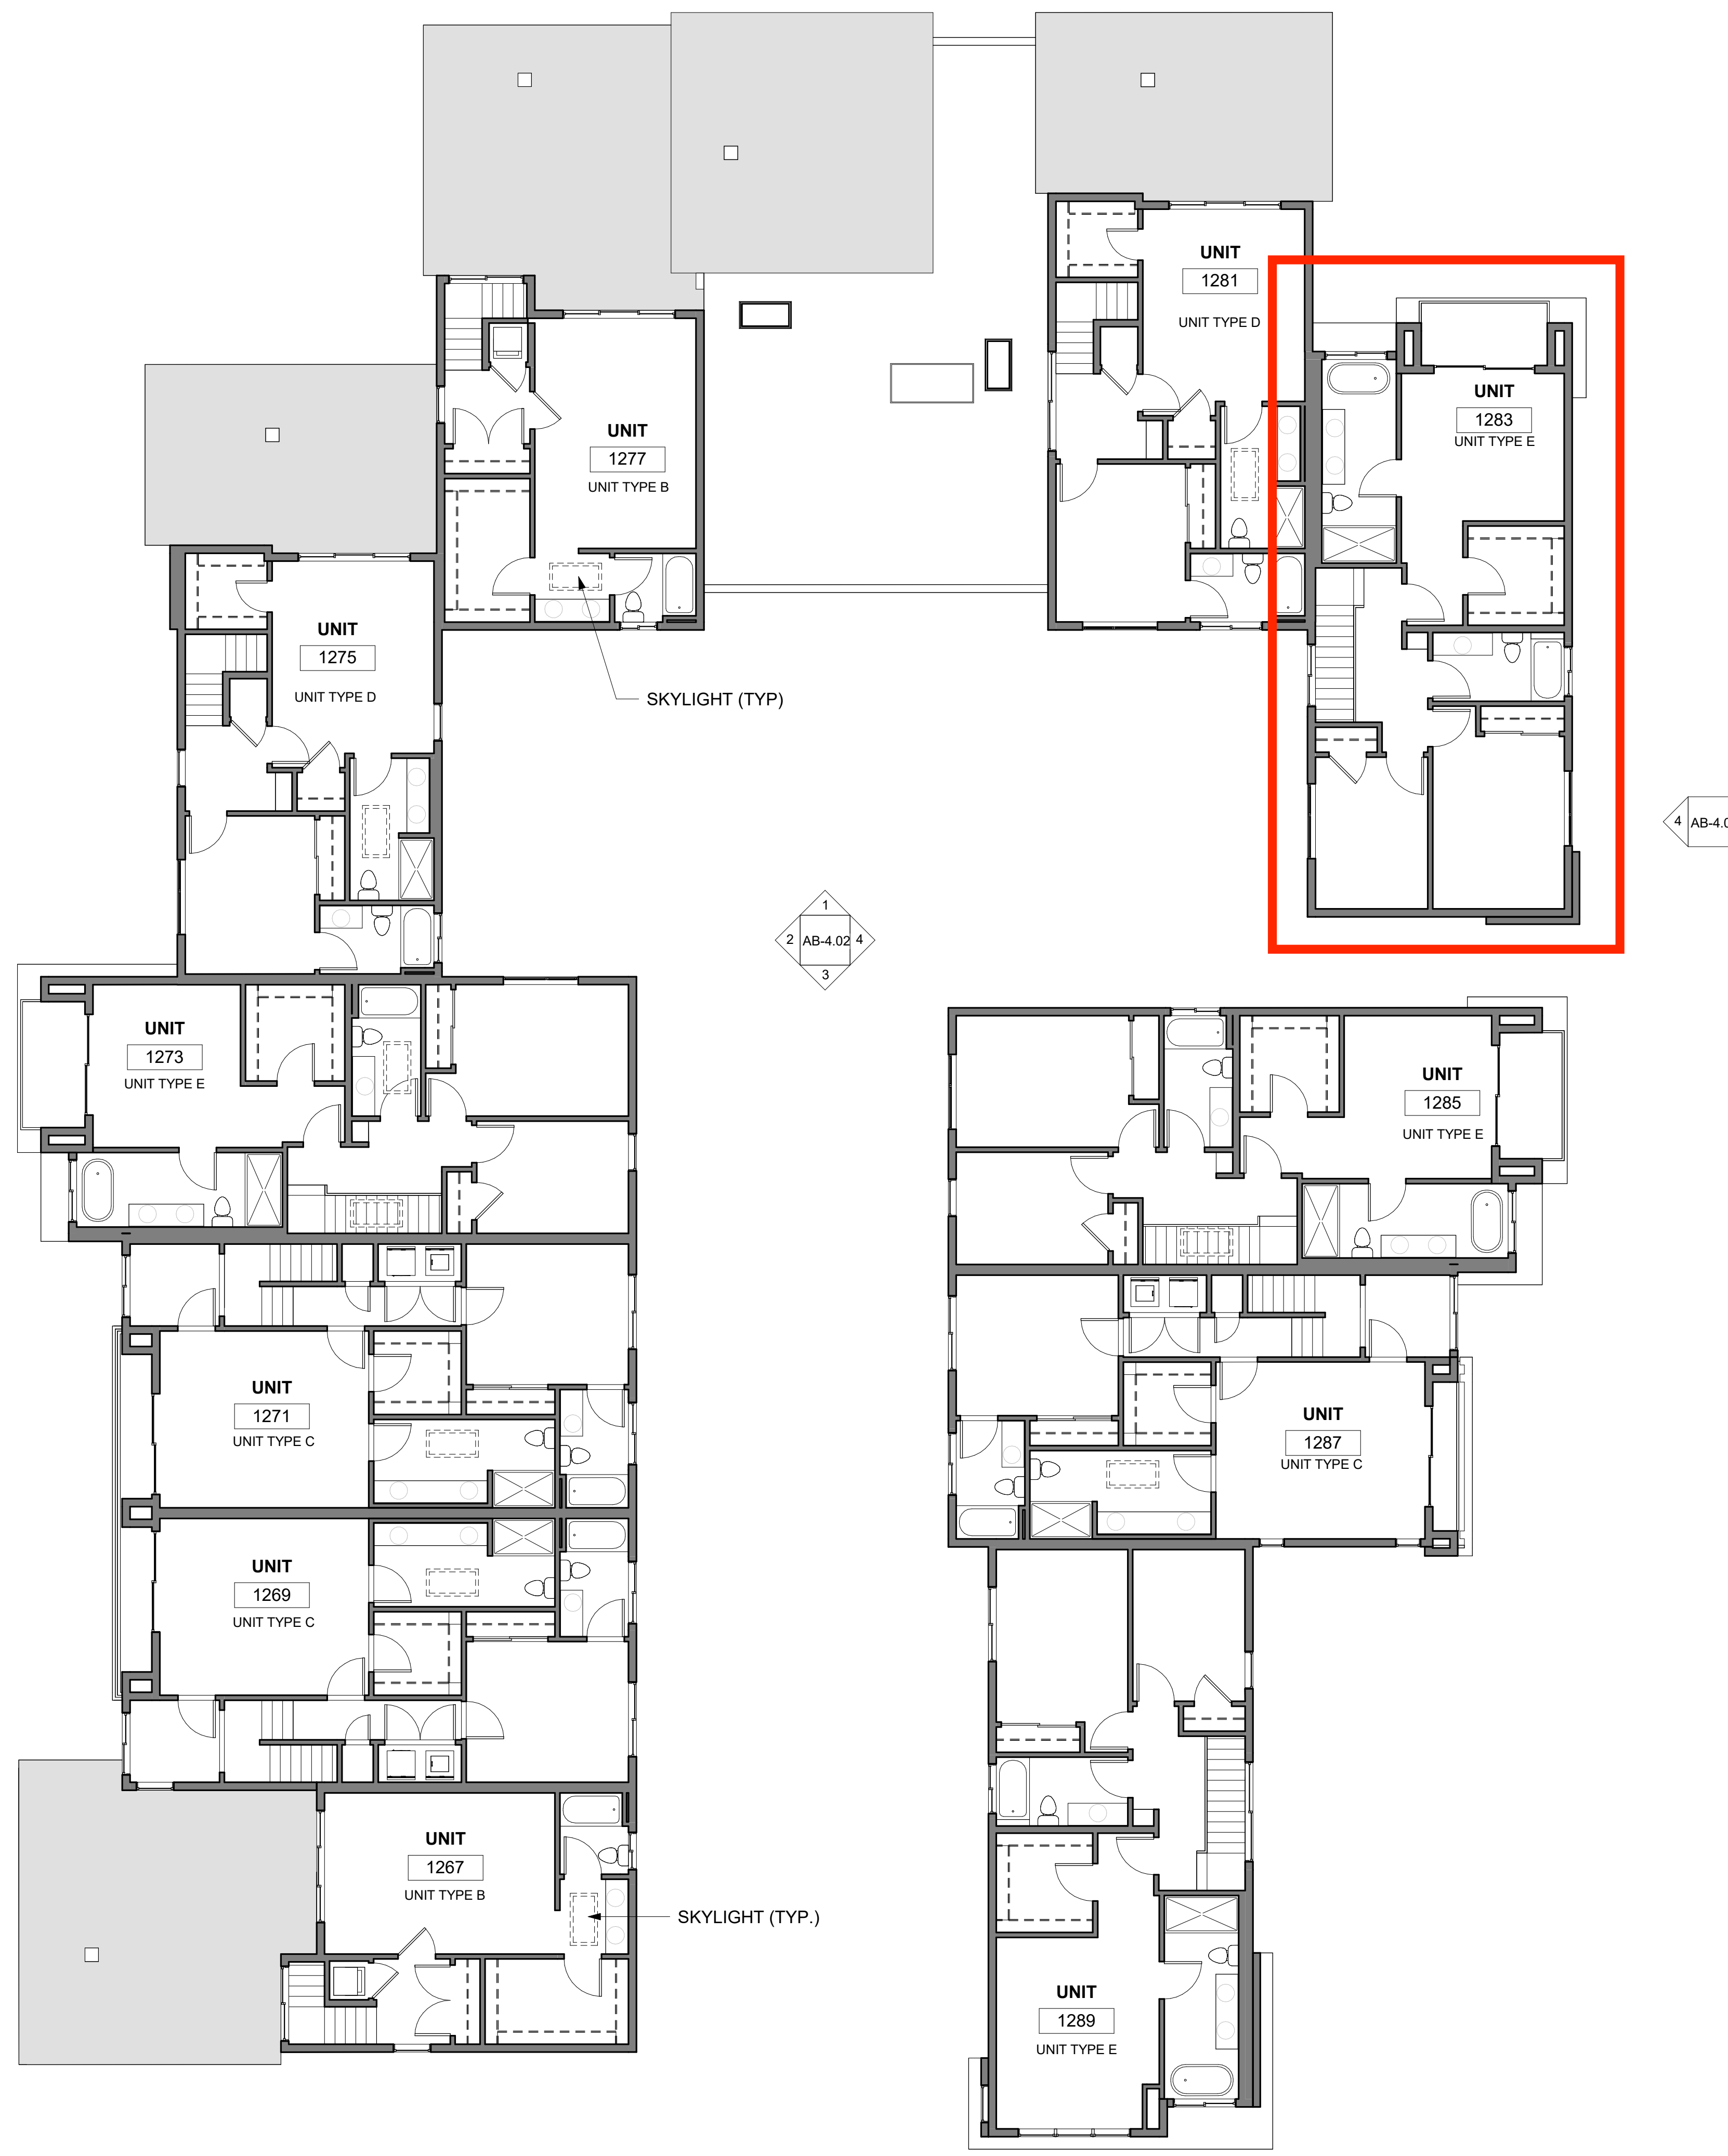


3
AB-4.01

4
AB-4.01

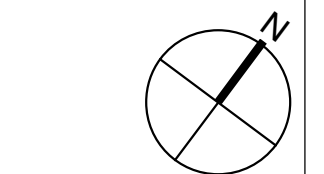

2ND FLOOR @ BLDG 8
SCALE: 1/8" = 1'-0" 1

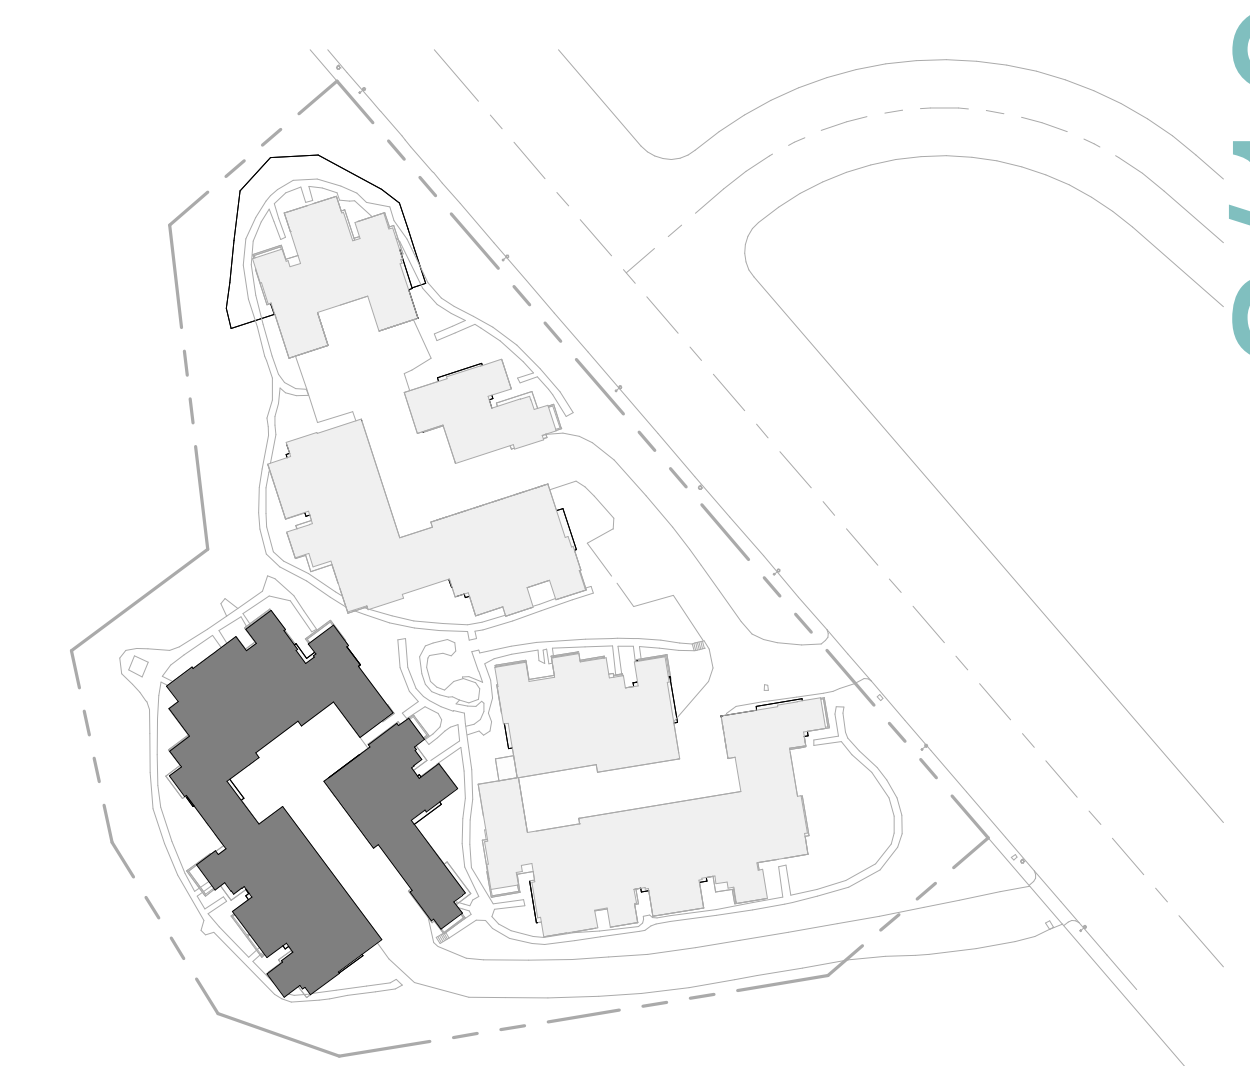


KEY PLAN

3/10/2026 SD OPTION 2 PROGRESS SET

AB-2.03	Project No: 2532	By: Author	Scale: As indicated	2ND FLOOR @ BLDG 8	100% SCHEMATIC DESIGN 2/19/2026	SYCHOA TOWNHOMES 1267-1337 PALISADES DRIVE PACIFIC PALISADES, CA 90272	dfh architecture interior environments 1344 20th Street S#4, CA 1-310-394-4043 info@dfhaa.com www.dfhaa.com
---------	---------------------	------------	------------------------	--------------------	------------------------------------	--	--



B8 WEST ELEVATION	SCALE:	4
	1/8" = 1'-0"	

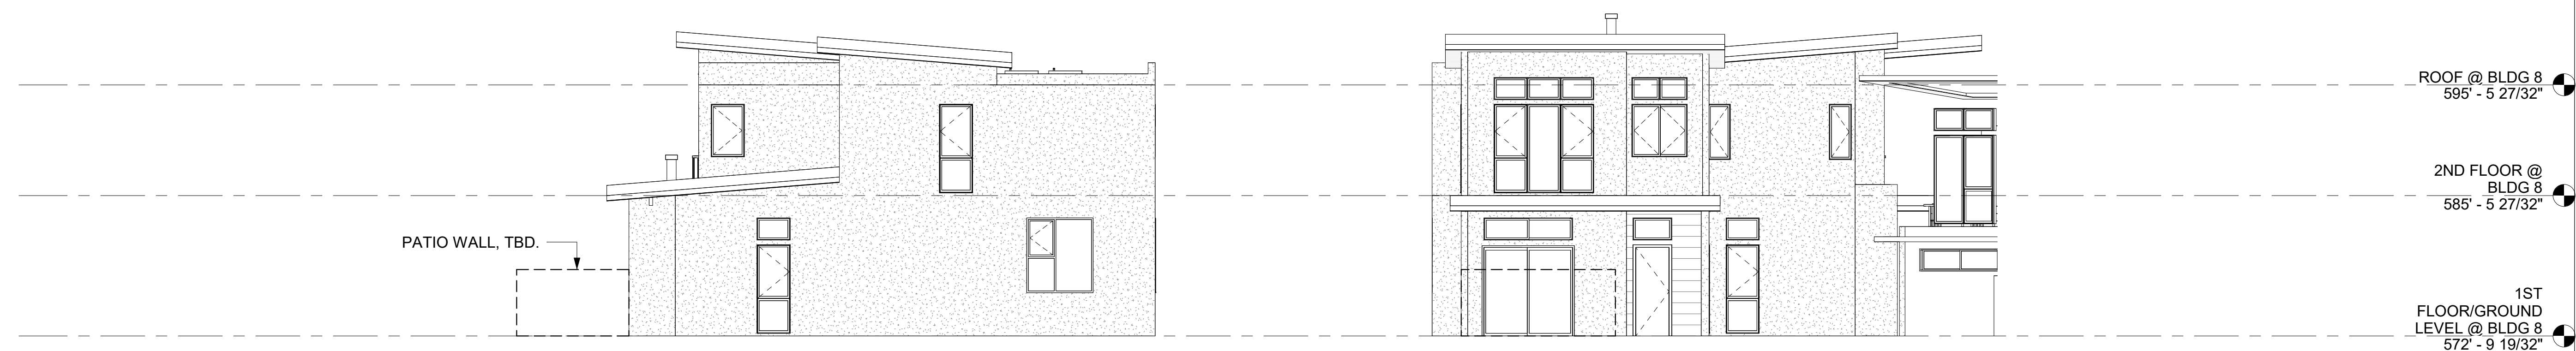

B8 SOUTH ELEVATION



B8 EAST ELEVATION	SCALE:	2
	1/8" = 1'-0"	



B8 NORTH ELEVATION

Side

Front

1-310.394.4045
info@dfhaia.com
www.dfhaia.com

architecture
interiors
entitlements

atn
architects

STATION TOWNHOMES
1267-1337 PALISADES DRIVE
PACIFIC PALISADES, CA 90272

100% SCHEMATIC DESIGN

EXTERIOR ELEVATIONS
@ BLDG 8

Scale: 1/8" = 1'-0"

By: Author

Project No: 2532


B-4.01

3/10/2026 SD OPTION 2 PROGRESS SET


8/10/2026 1:40:22 PM



B8 COURTYARD WEST ELEVATION

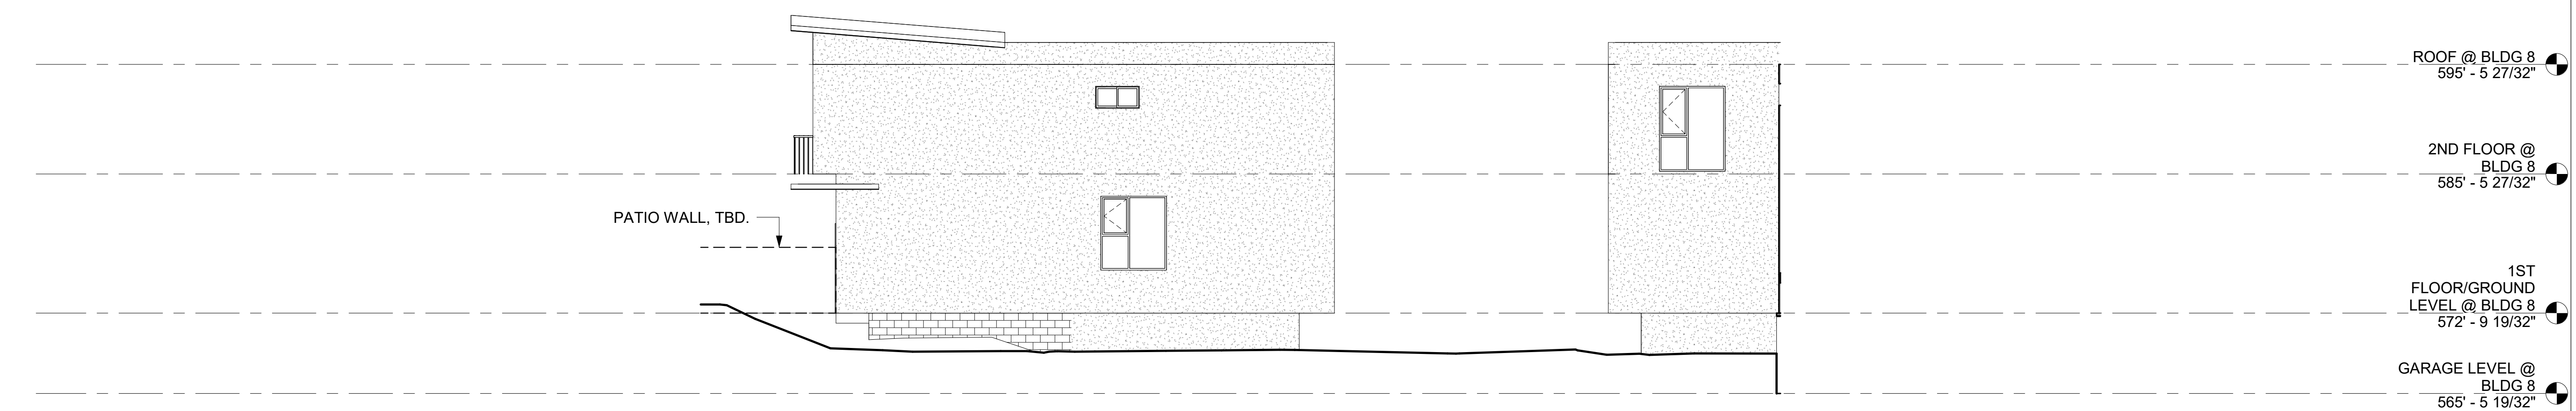

B8 COURTYARD SOUTH ELEVATION

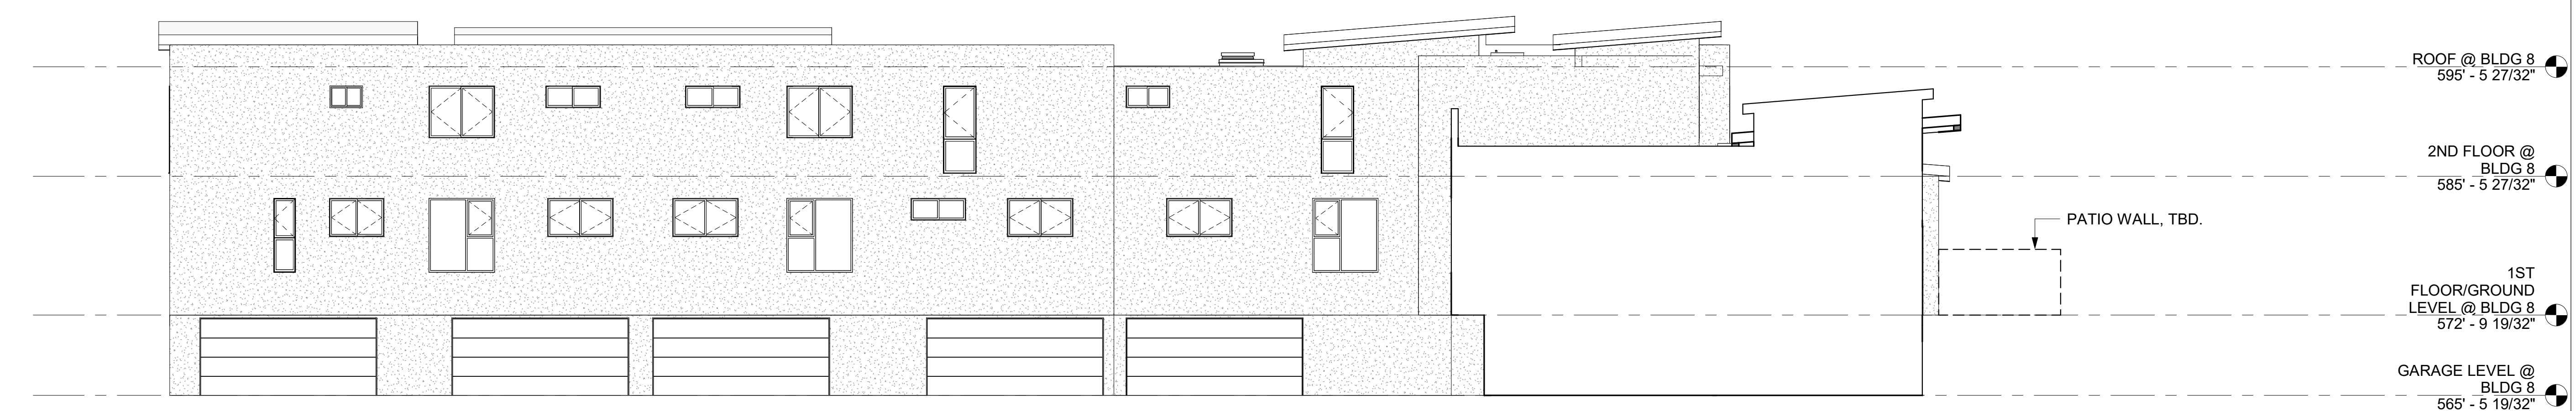

B8 COURTYARD EAST ELEVATION	SCALE: 1/8" = 1'-0" 2
---	--



B8 COURTYARD NORTH ELEVATION SCALE: $\frac{1}{8}" = 1'-0"$ **1**



10/10/2026 1:40:23 PM

Side

Rear

3/10/2026 SD OPTION 2 PROGRESS SET

3/10/2026 SD OPTION 2 PROGRESS SET

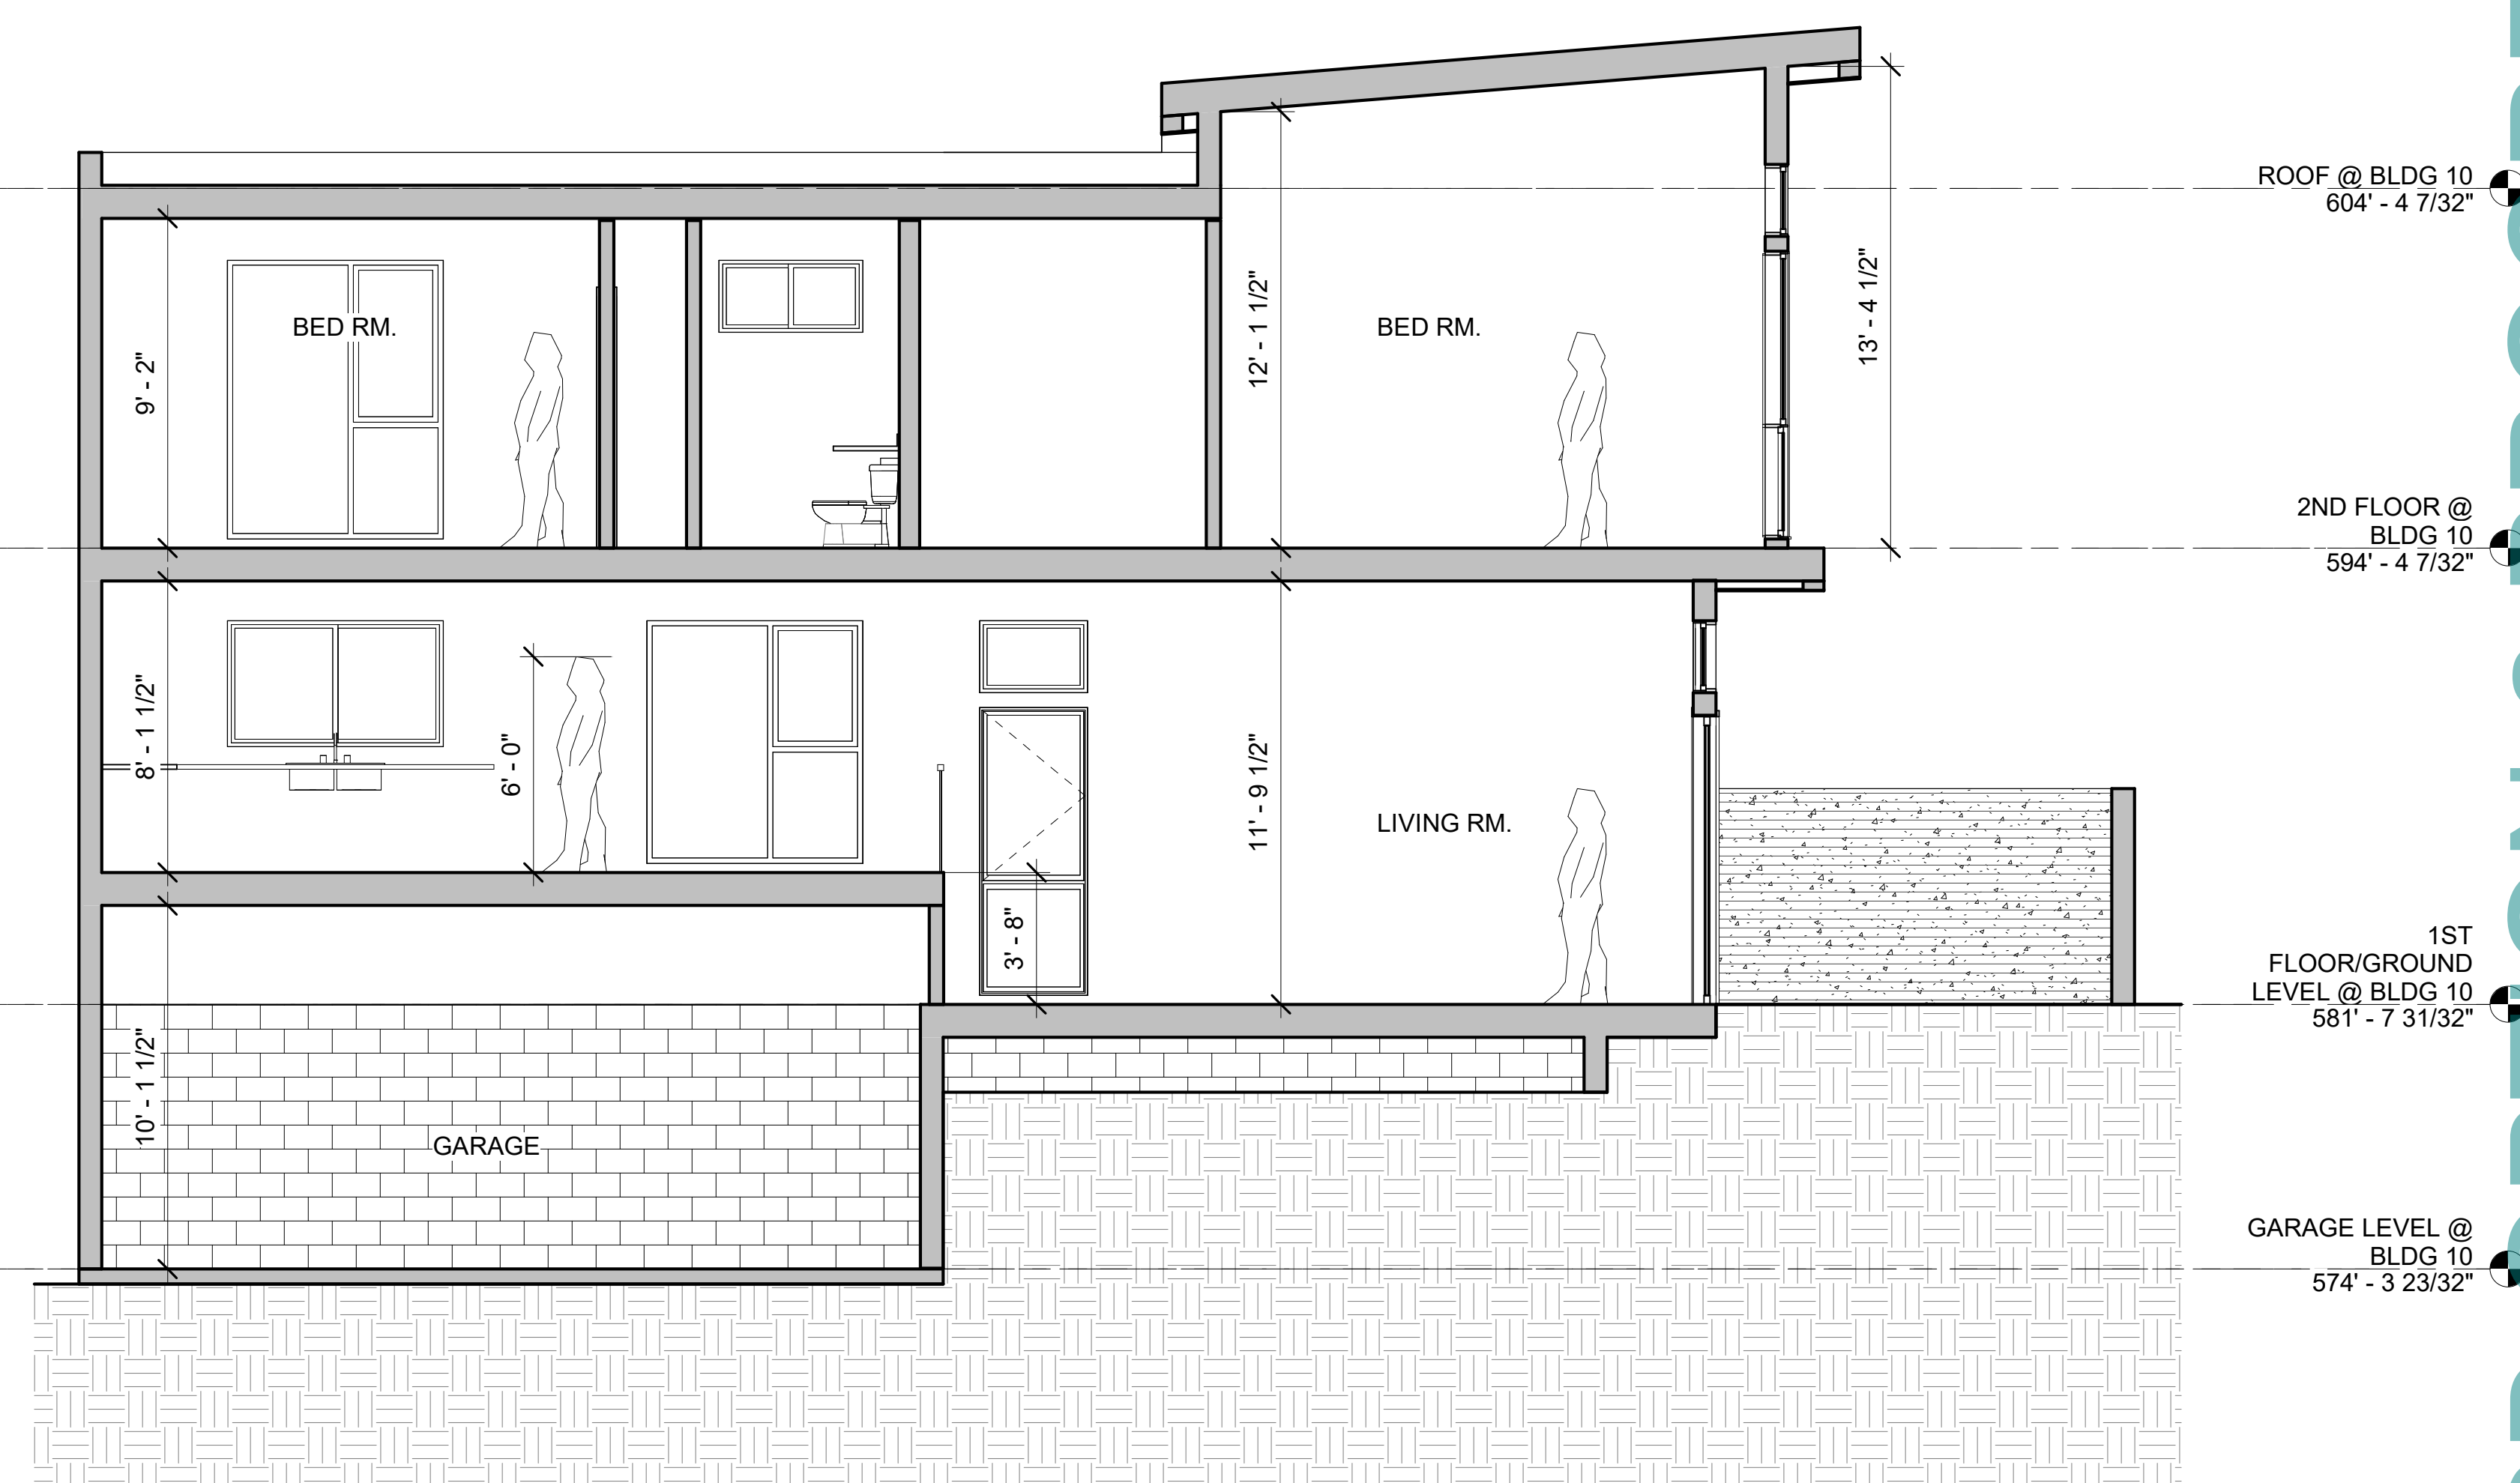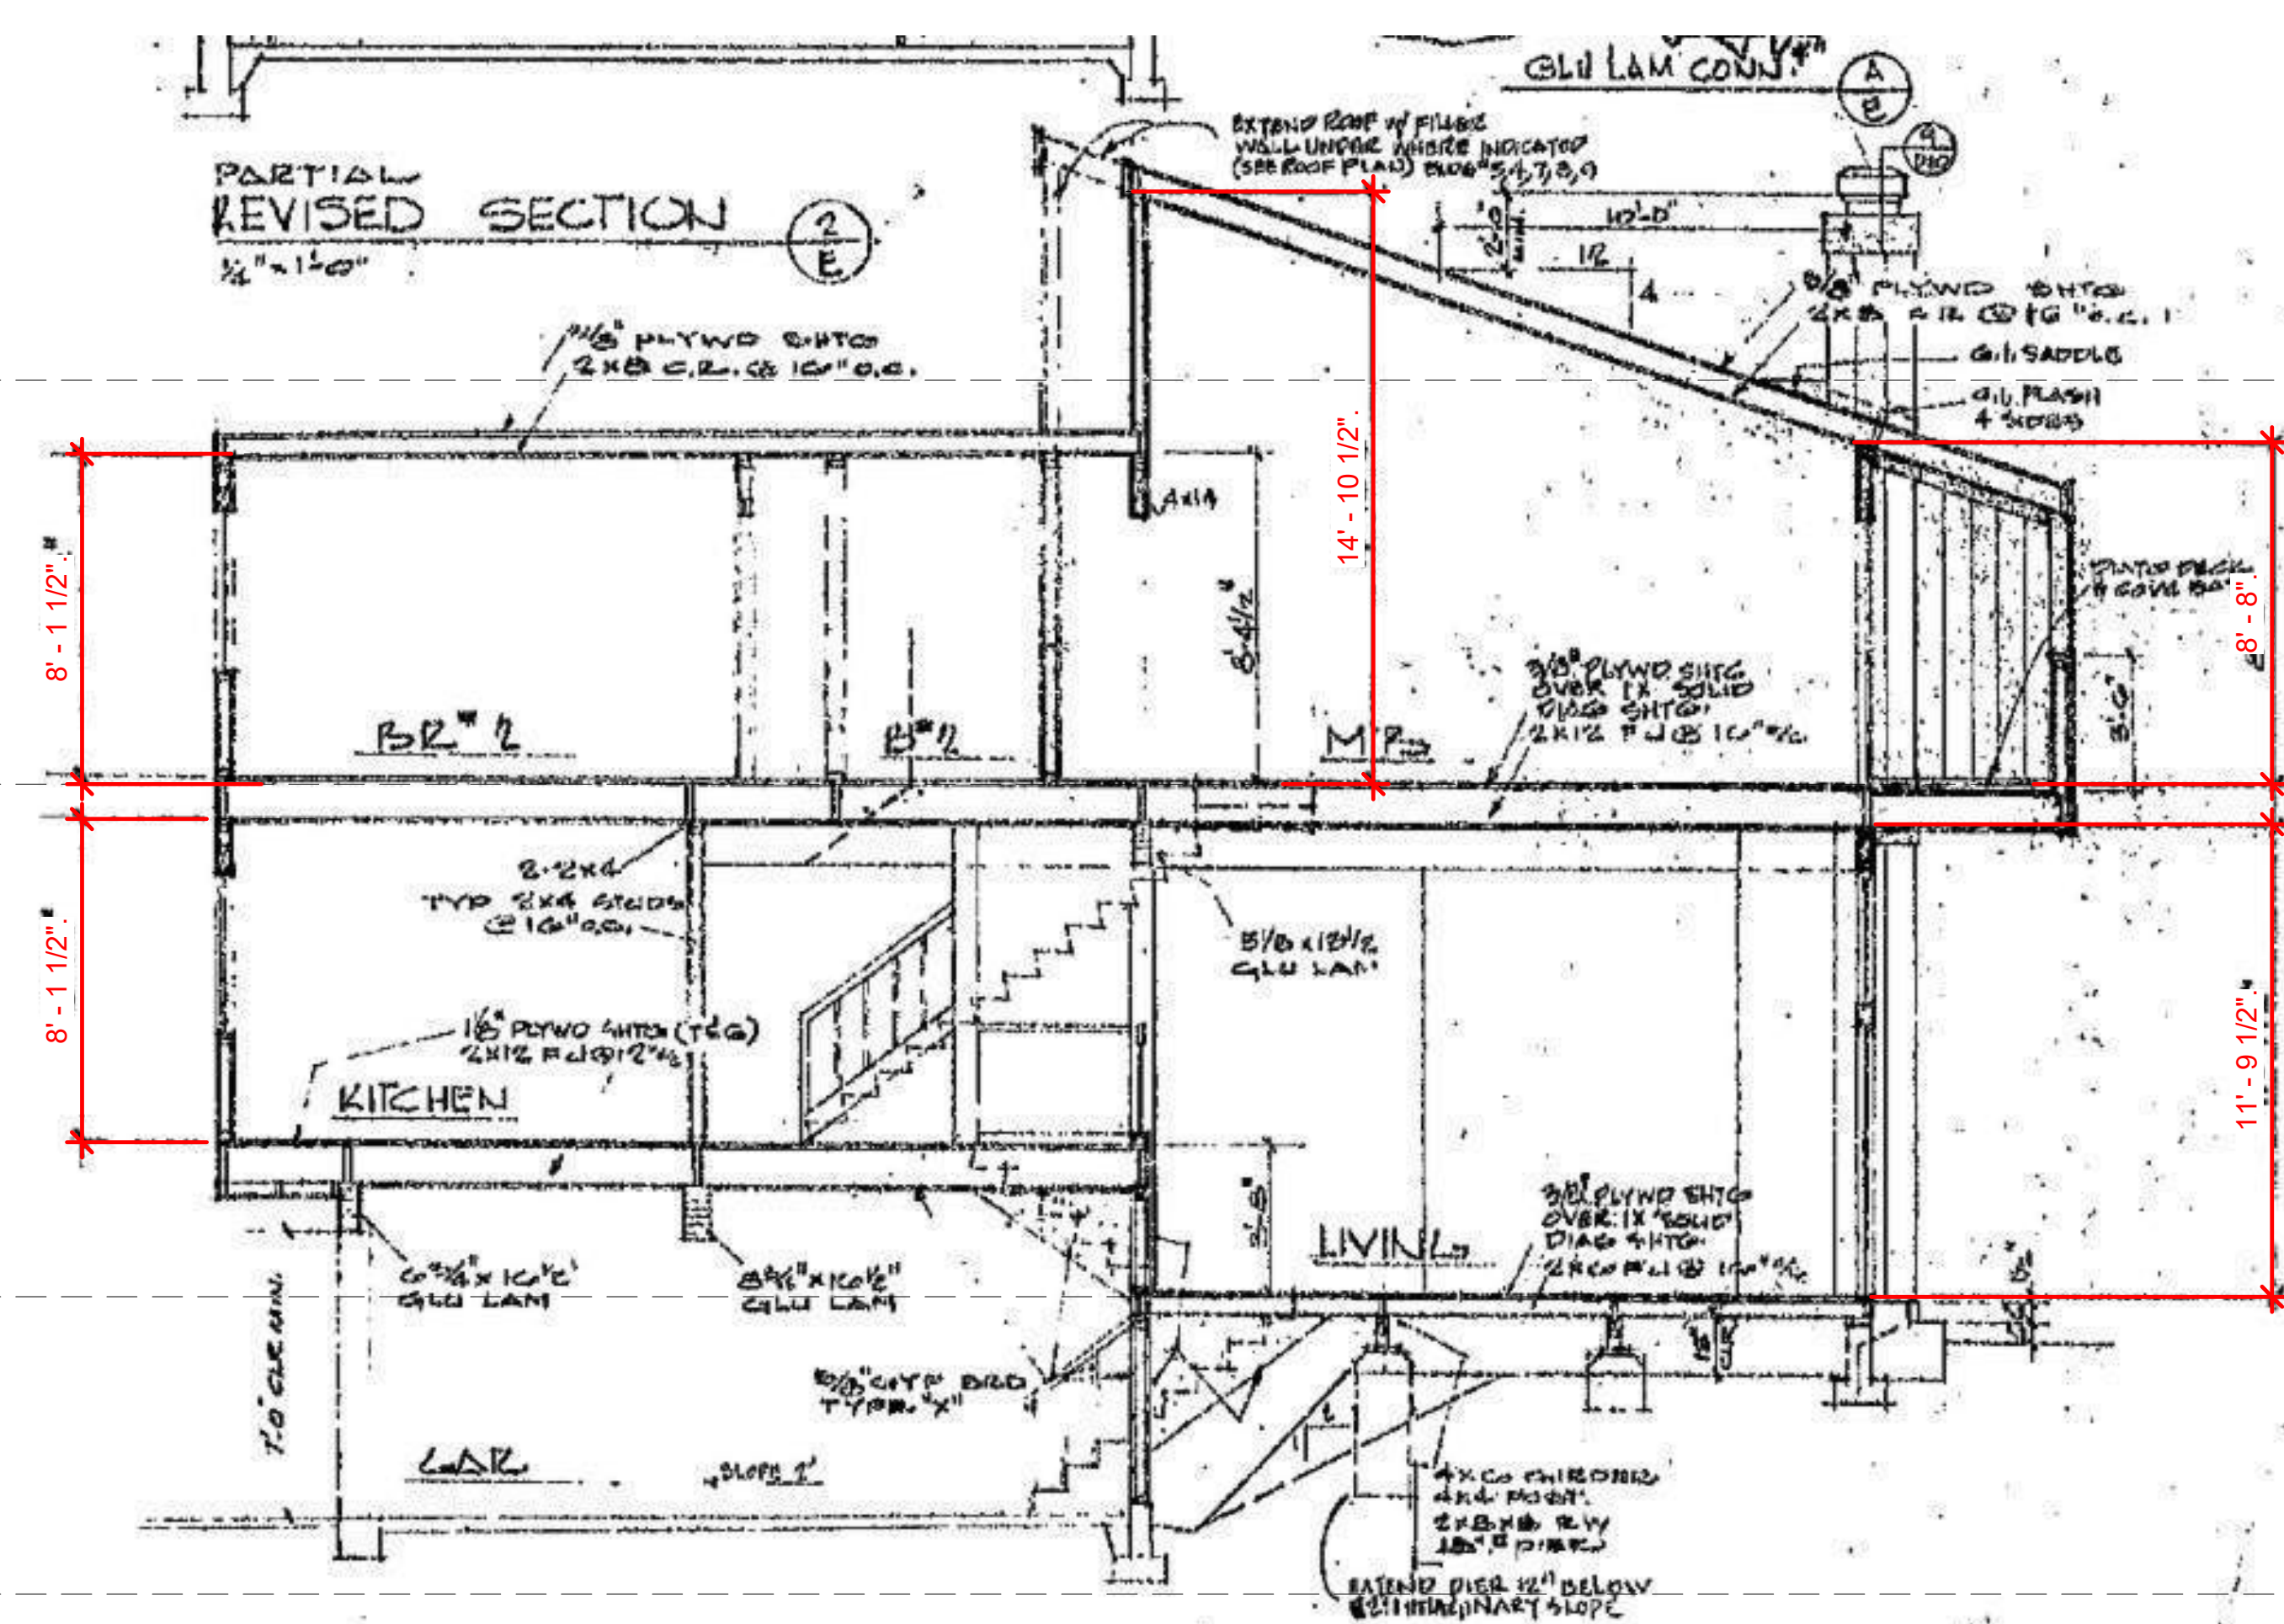

TYPICAL UNIT SECTION

SCALE: $\frac{1}{4}" = 1'-0"$ 1