






Unit type 'E'
without balcony

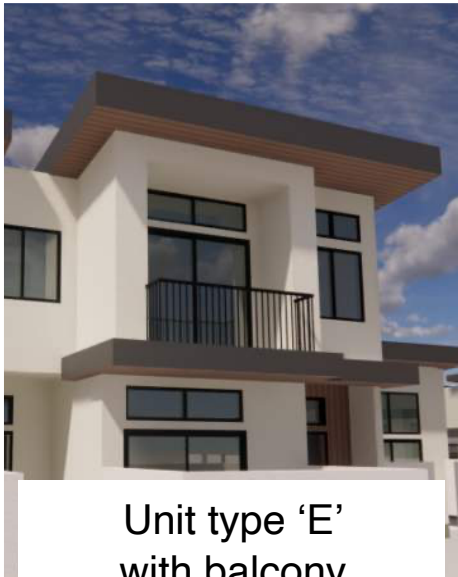

Unit type 'E'
with balcony

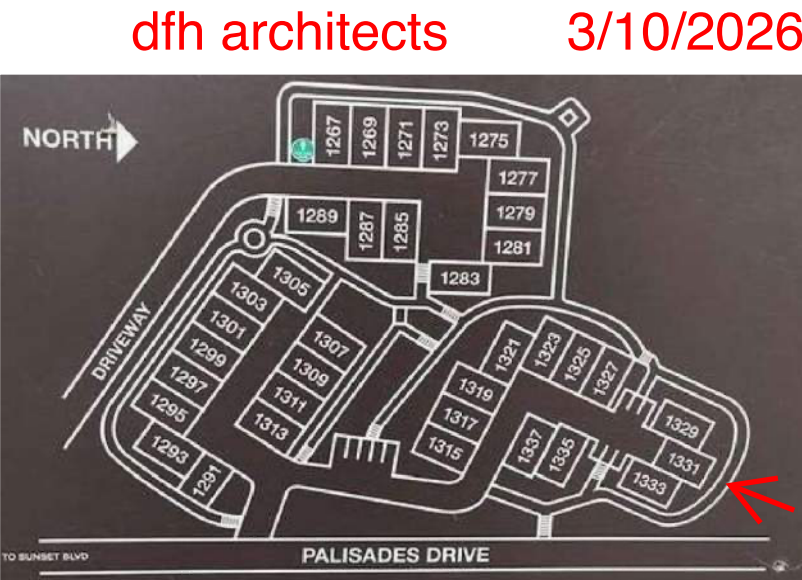

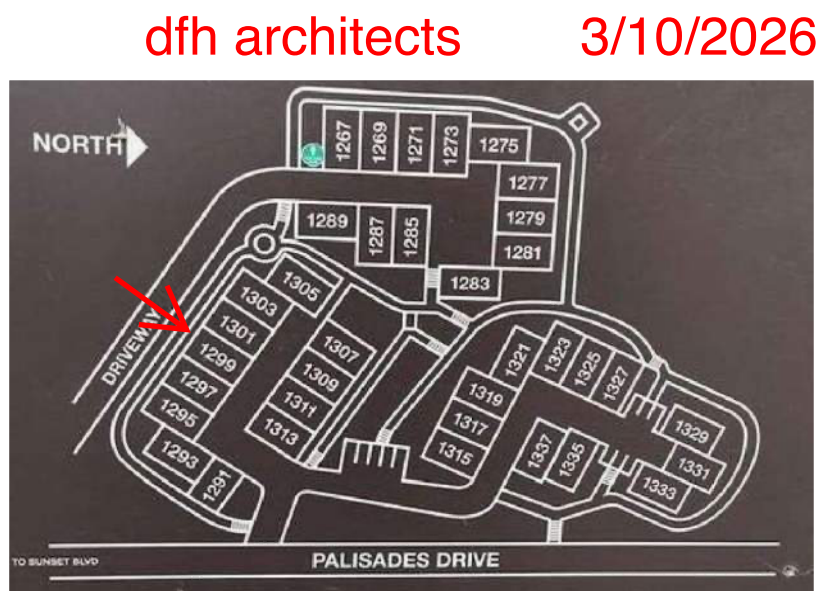


3/10/2026 1:40:05 PM



3/10/2026 SD OPTION 2 PROGRESS SET

1344 20th Street S4, CA 1-910-394-4045 info@dfhaa.com www.dfhaa.com		SYCHOA TOWNHOMES	100% SCHEMATIC DESIGN	PROPOSED SITE PLAN	Scale: 1" = 20'-0"	By: Author	Project No: 2532	A-1.02
		1267-1337 PALISADES DRIVE PACIFIC PALISADES, CA 90272						


3/10/2026 1:40:04 PM

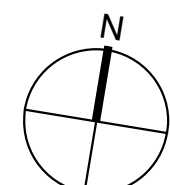

GARAGE LEVEL @ BLDG 7

SCALE:
1/8" = 1'-0"

1

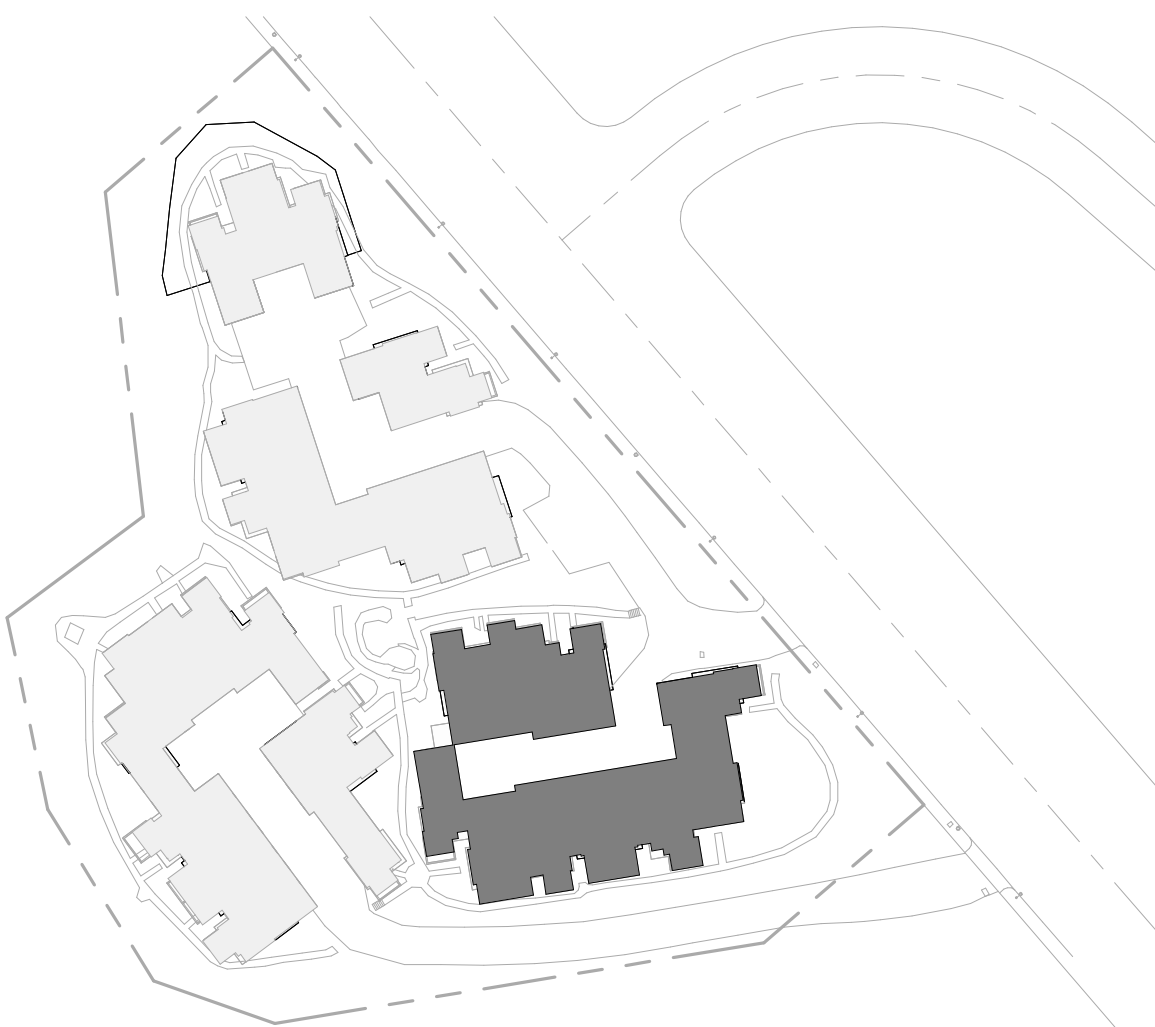


KEY PLAN



3/10/2026 SD OPTION 2 PROGRESS SET

AA-2.01	Project No: 2532	By: Author	Scale: As indicated	GARAGE LEVEL @ BLDG 7	100% SCHEMATIC DESIGN 2/19/2026	SYCHOA TOWNHOMES 1267-1337 PALISADES DRIVE PACIFIC PALISADES, CA 90272	dfh architecture interior environments 1344 20th Street S4, CA 1-310-394-4043 info@dfhaa.com www.dfhaa.com
---------	---------------------	------------	------------------------	--------------------------	------------------------------------	--	---

3/10/2026 1:40:05 PM

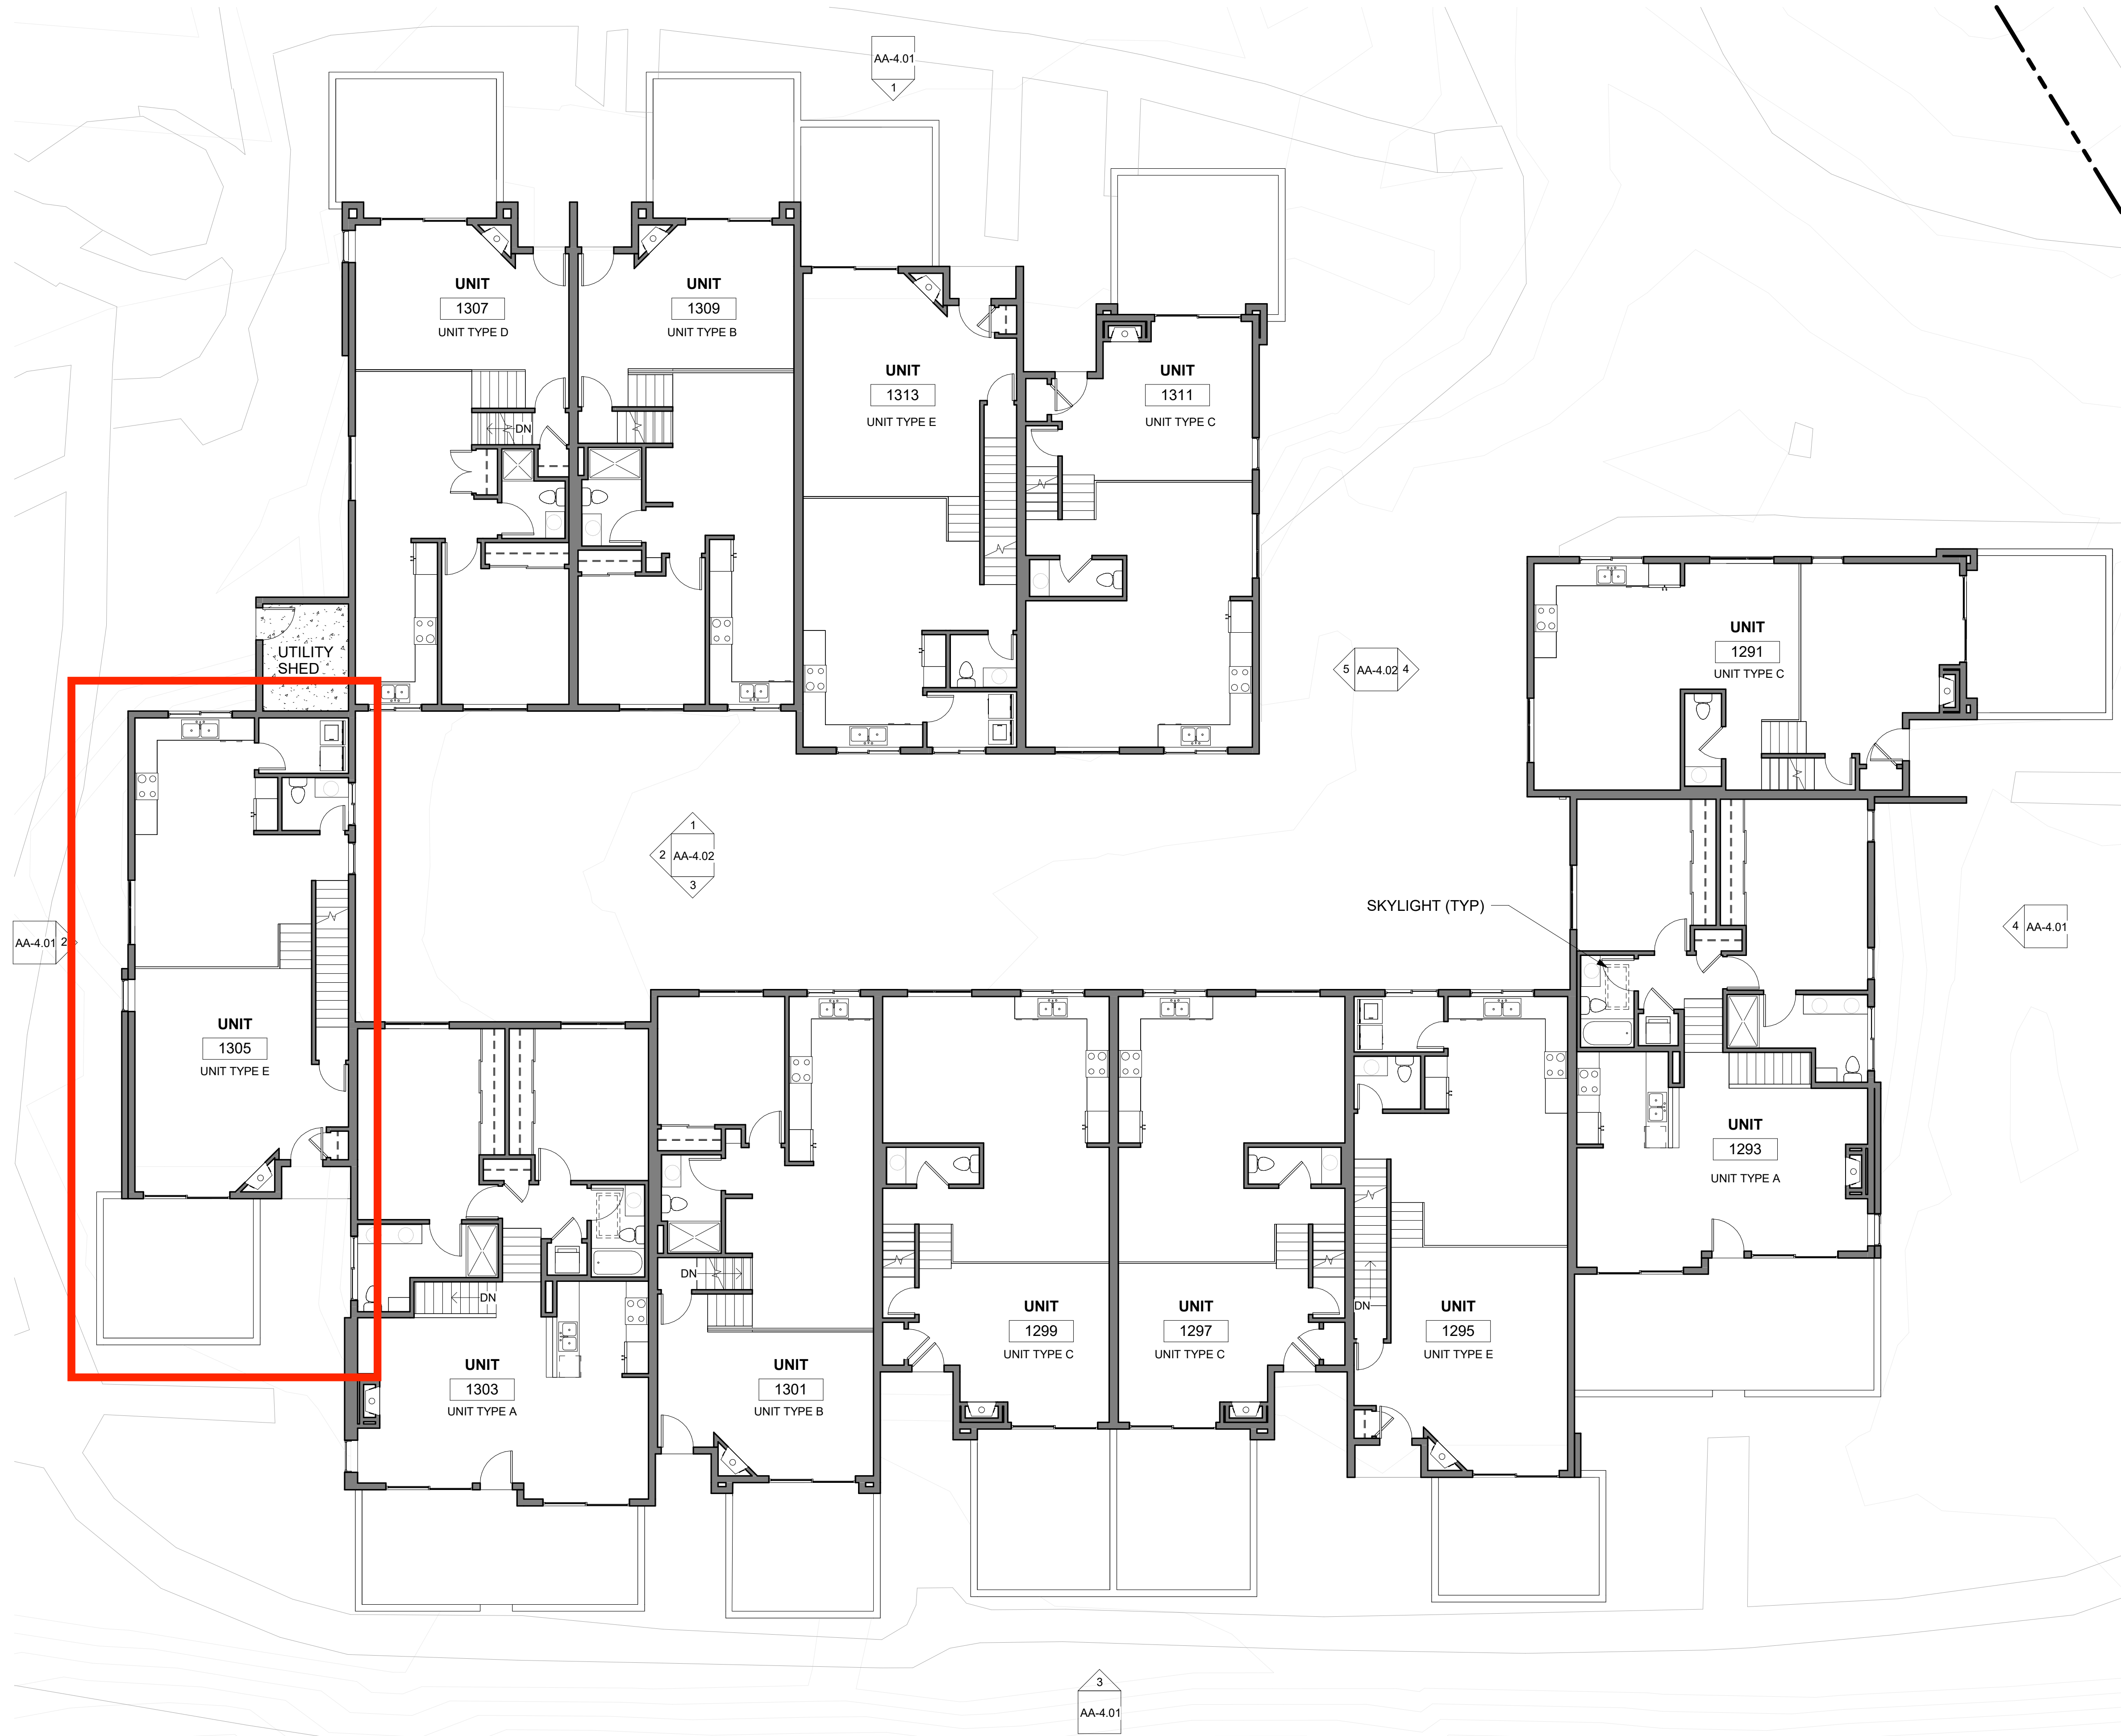

1ST FLOOR/GROUND LEVEL @ BLDG 7

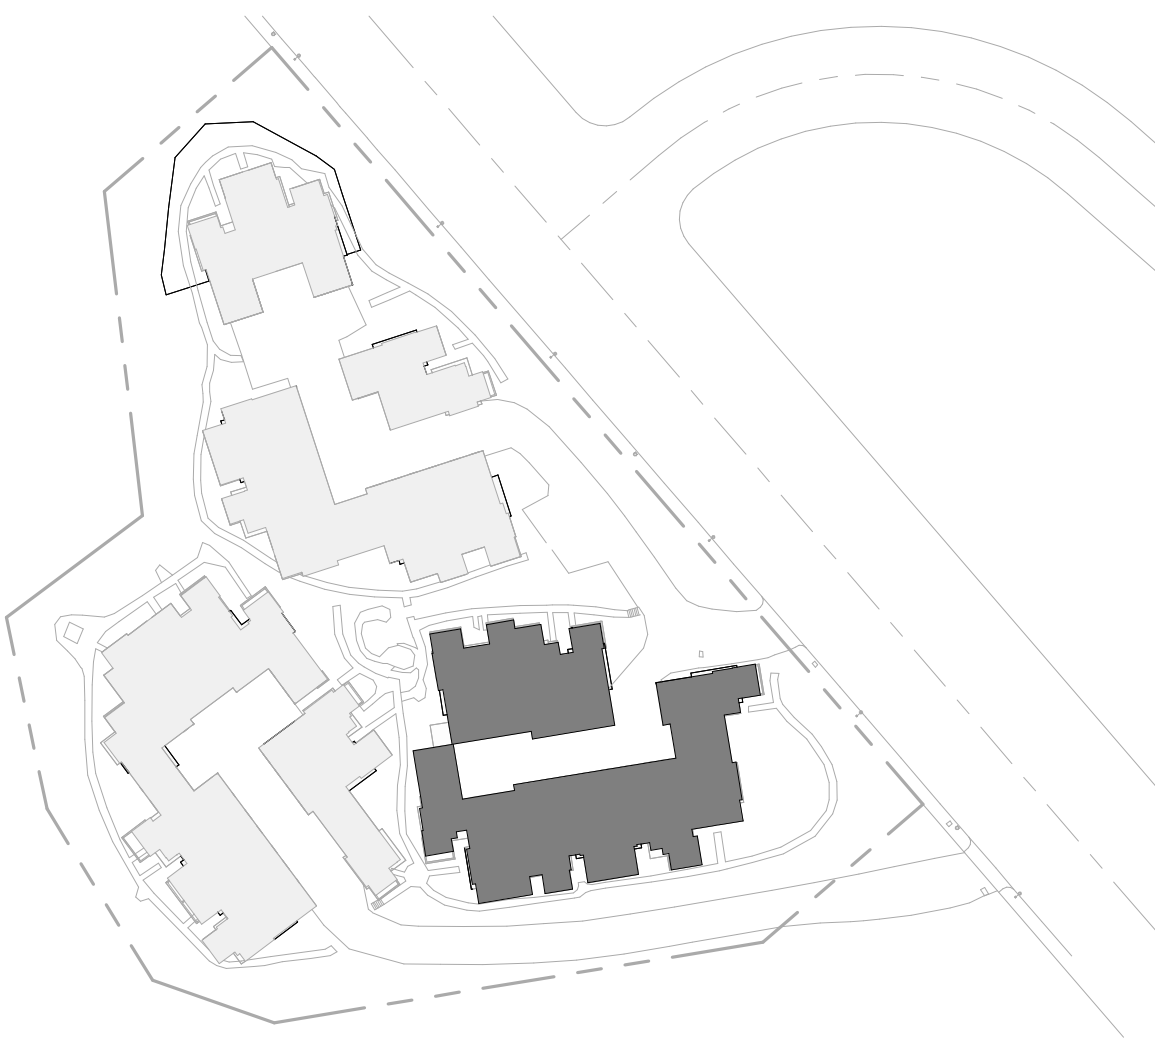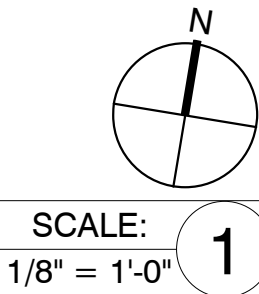


KEY PLAN

3/10/2026 SD OPTION 2 PROGRESS SET

SYCHOA TOWNHOMES 1267-1337 PALISADES DRIVE PACIFIC PALISADES, CA 90272		100% SCHEMATIC DESIGN 2/19/2026		1ST FLOOR PLAN/GROUND LEVEL @ BLDG 7		AA-2.02	
dfh architecture interior environments		1344 20th Street S4, CA 1-818-394-4045 info@dfhaa.com www.dfhaa.com		Scale: As indicated		By: Author	
				Project No: 2532			

3/10/2026 1:40:07 PM

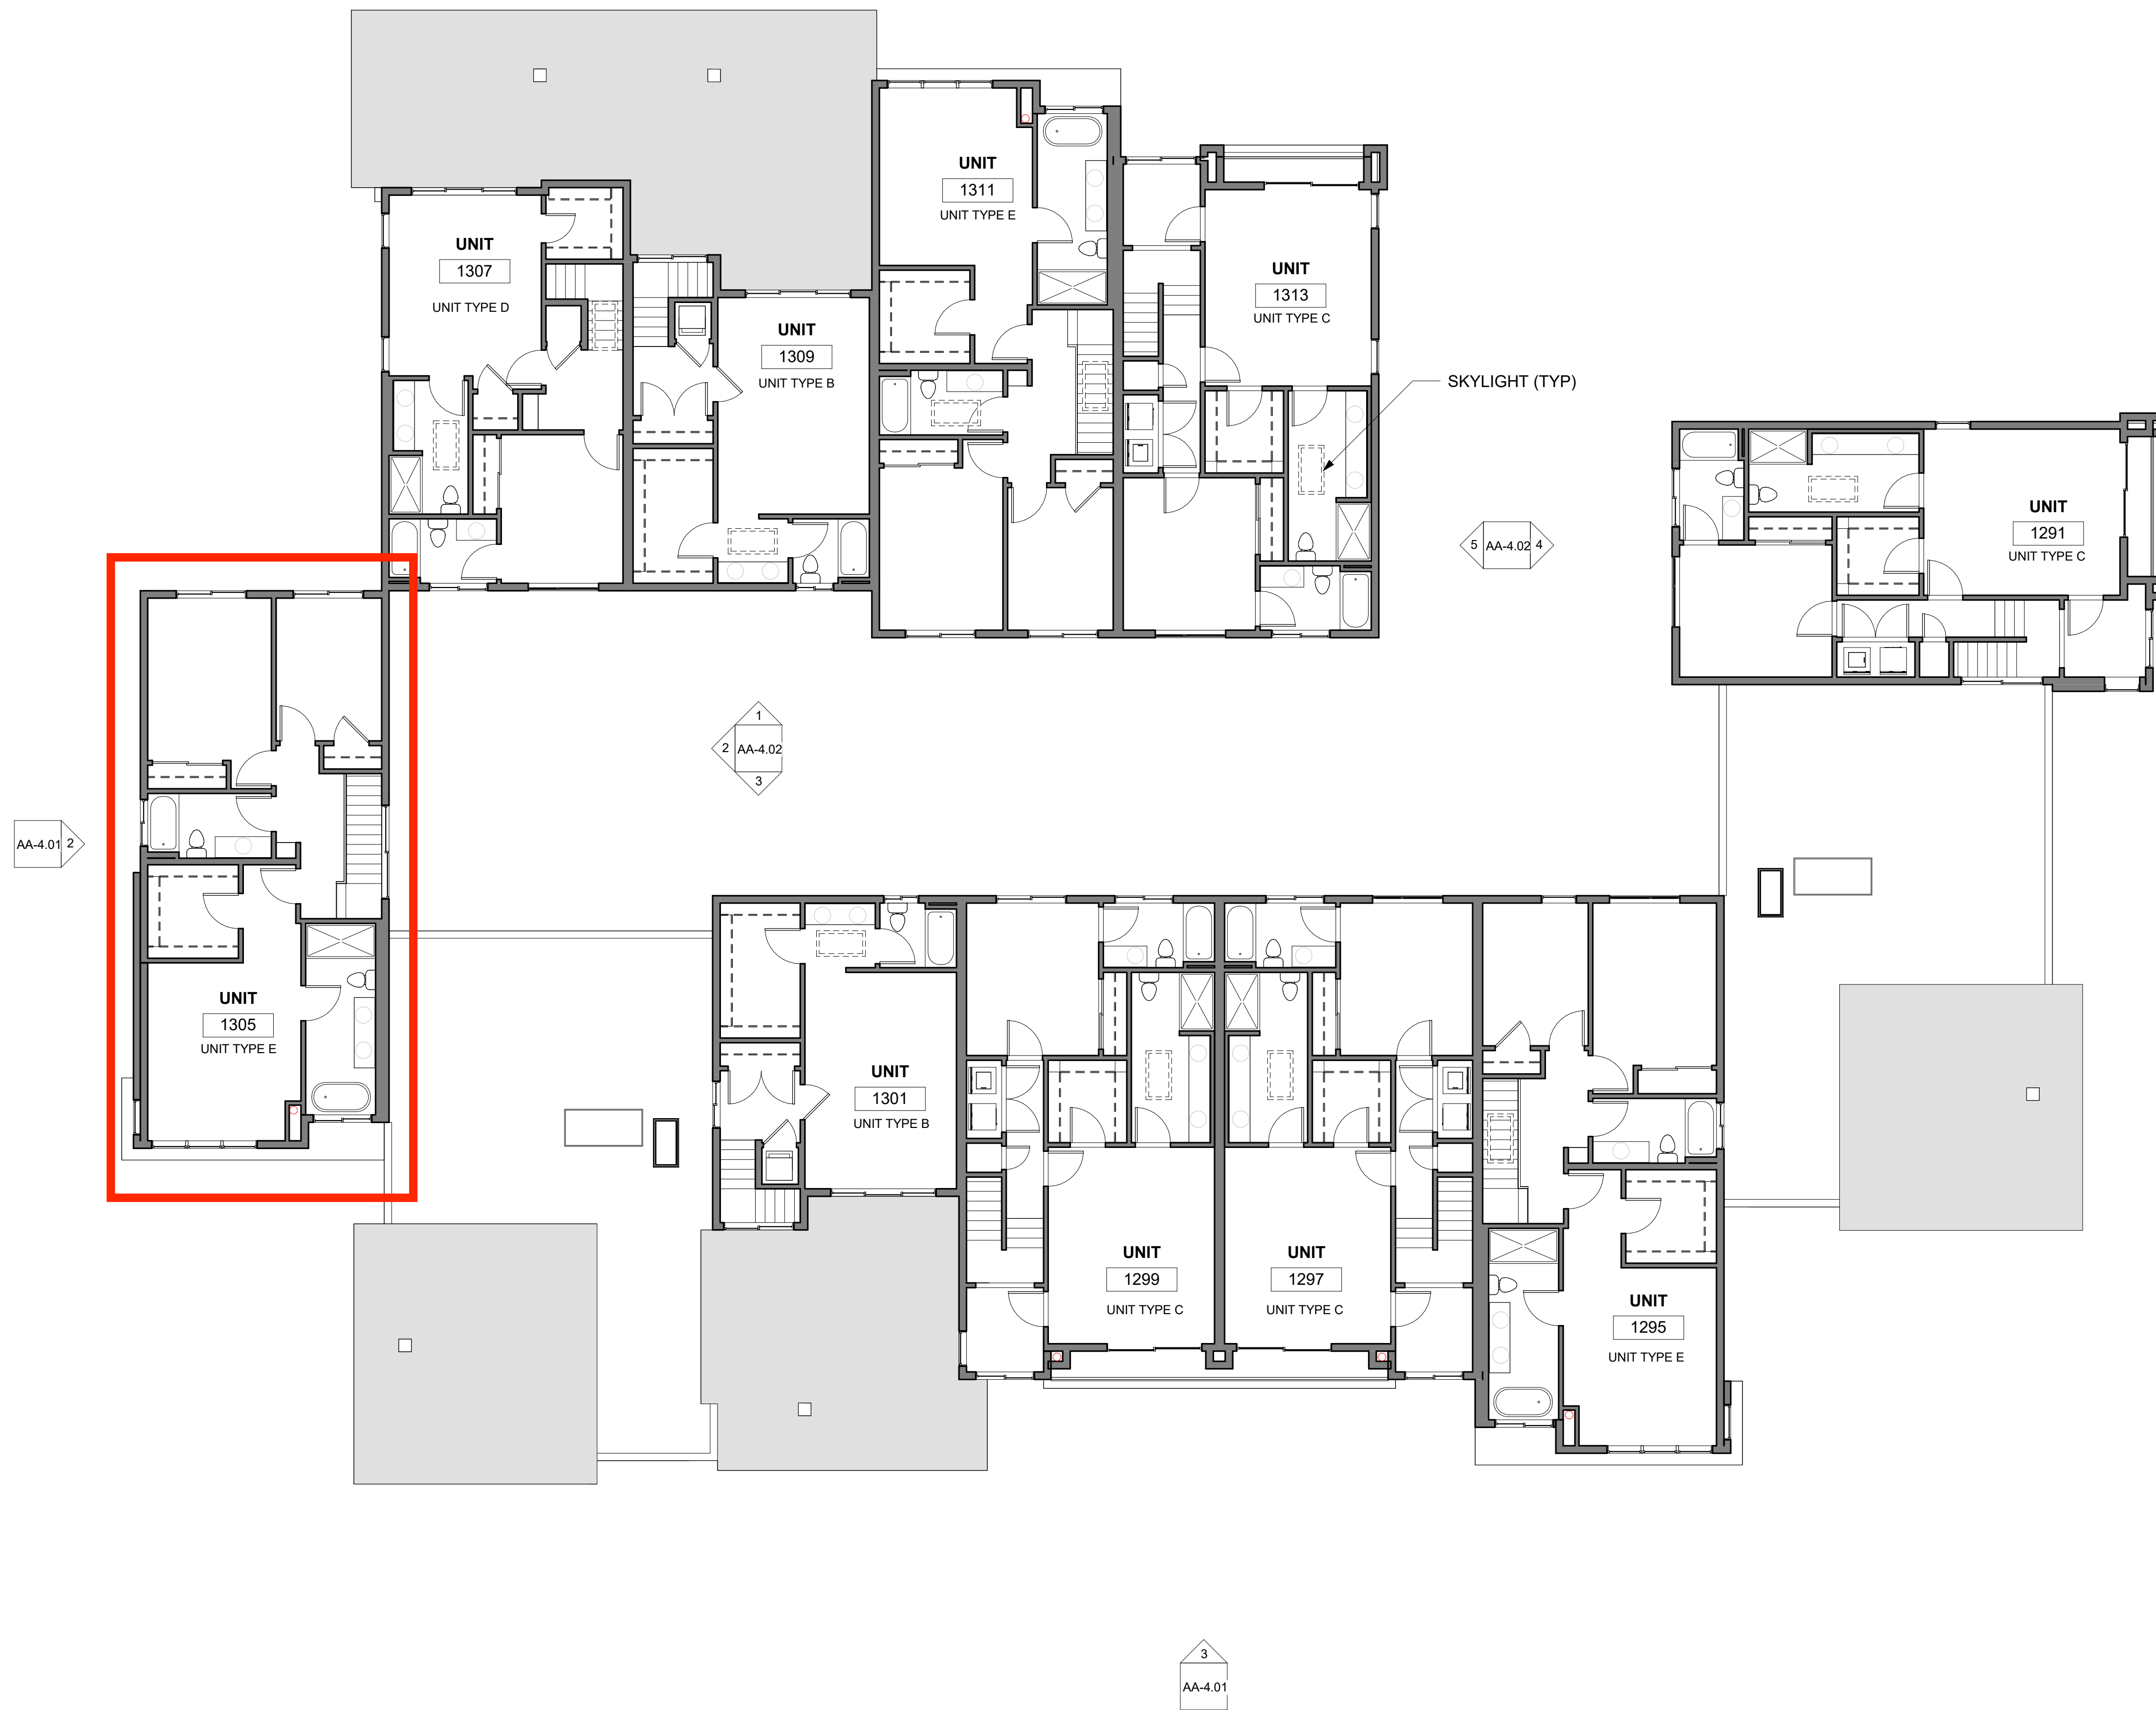

2ND FLOOR @ BLDG 7

SCALE:
1/8" = 1'-0"

1



KEY PLAN

3/10/2026 SD OPTION 2 PROGRESS SET

SYCHOA TOWNHOMES 1267-1337 PALISADES DRIVE PACIFIC PALISADES, CA 90272		100% SCHEMATIC DESIGN 2/19/2026		2ND FLOOR @ BLDG 7		AA-2.03	
dfh architecture interior environments		1344 20th Street S#4, CA 1-310-394-4043 info@dfhaa.com www.dfhaa.com		Scale: As indicated		By: Author	
						Project No: 2532	

3/10/2026 1:42:26 PM



B7 PALISADES DRIVE EAST ELEVATION

SCALE: 1/8" = 1'-0" 4

Front



B7 SOUTH ELEVATION

SCALE: 1/8" = 1'-0" 3

Side



B7 WEST ELEVATION

SCALE: 1/8" = 1'-0" 2

Rear



B7 NORTH ELEVATION

SCALE: 1/8" = 1'-0" 1

3/10/2026 SD OPTION 2 PROGRESS SET

SYCHOA TOWNHOMES
1267-1337 PALISADES DRIVE
PACIFIC PALISADES, CA 90272

100% SCHEMATIC DESIGN
2/19/2026

EXTERIOR ELEVATIONS
@ BLDG 7

Scale:
1/8" = 1'-0"
By: Author
Project No:
2532

AA-4.01



SCALE:
 $\frac{1}{8"} = 1'-0"$



SCALE:
 $1/8" = 1'-0"$



SCALE:
 $1/8" = 1'-0"$

1ST
FLOOR/GROUND
LEVEL @ BLDG 7 
570' - 0"




SCALE:
1/8" = 1'-0"



SCALE:
 $1/8" = 1'-0"$

3/10/2026 1:40:27 PM

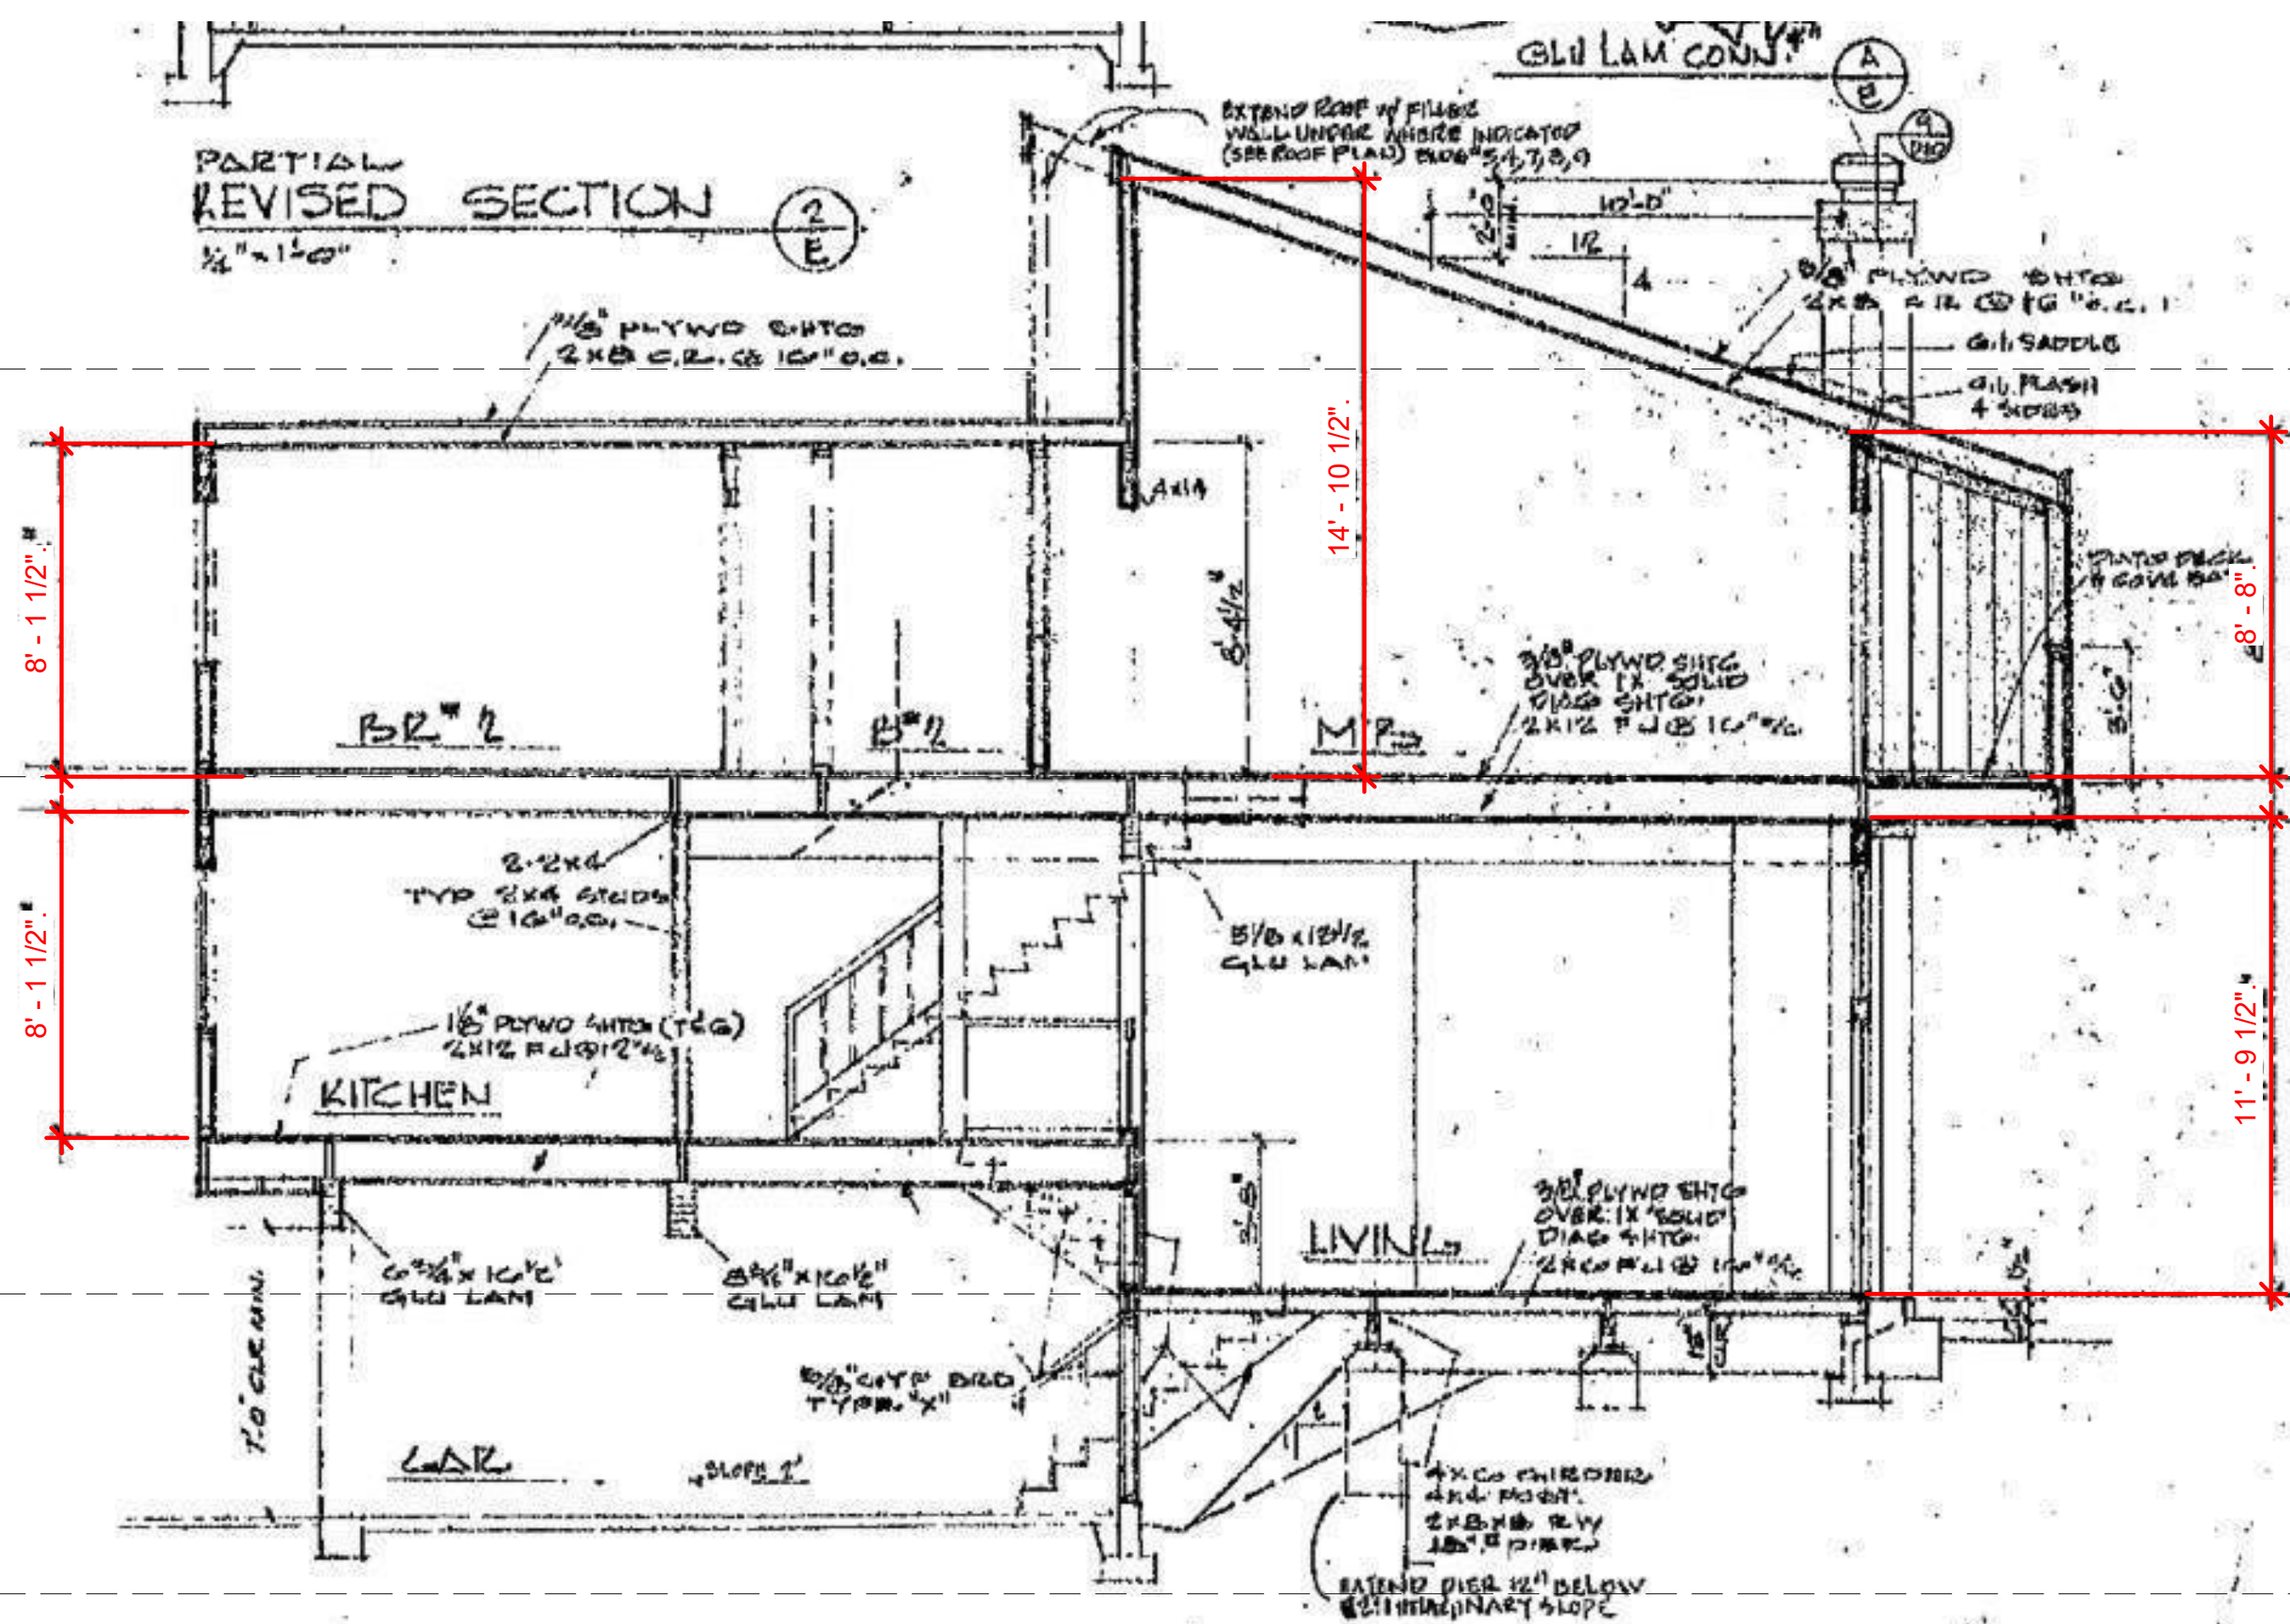

ROOF @ BLDG 10
604' - 4 7/32"

2ND FLOOR @
BLDG 10
594' - 4 7/32"

1ST
FLOOR/GROUND
LEVEL @ BLDG 10
581' - 7 31/32"

GARAGE LEVEL @
BLDG 10
574' - 3 23/32"

TYPICAL UNIT SECTION

SCALE:
1/4" = 1'-0"

1

3/10/2026 SD OPTION 2 PROGRESS SET

SYCHOA TOWNHOMES
1267-1337 PALISADES DRIVE
PACIFIC PALISADES, CA 90272

100% SCHEMATIC DESIGN
2/19/2026

BUILDING SECTIONS

AD-3.01